




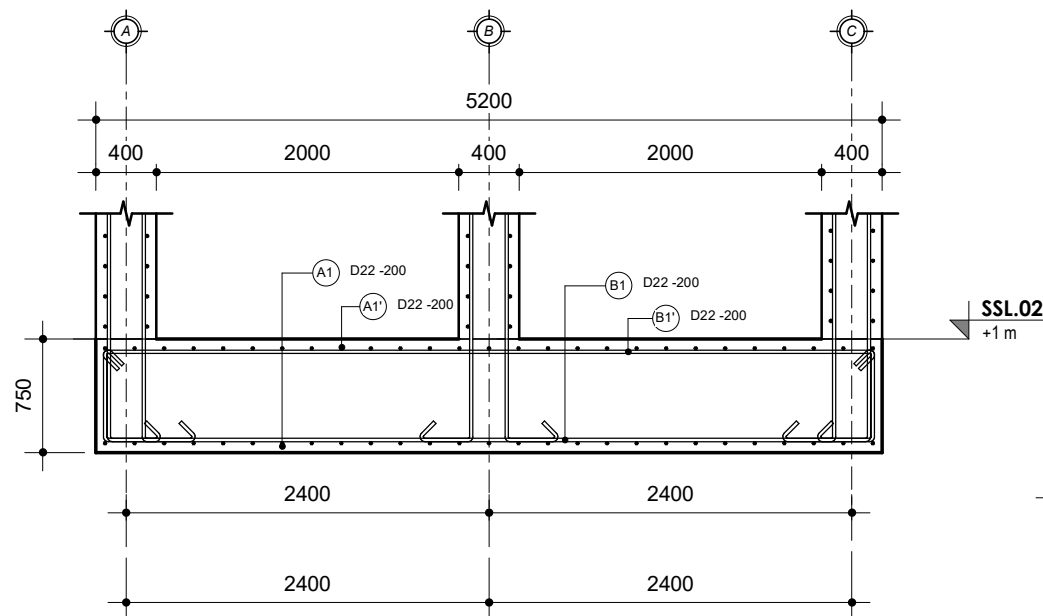


1 Potongan B - Floor Slab
1 : 50

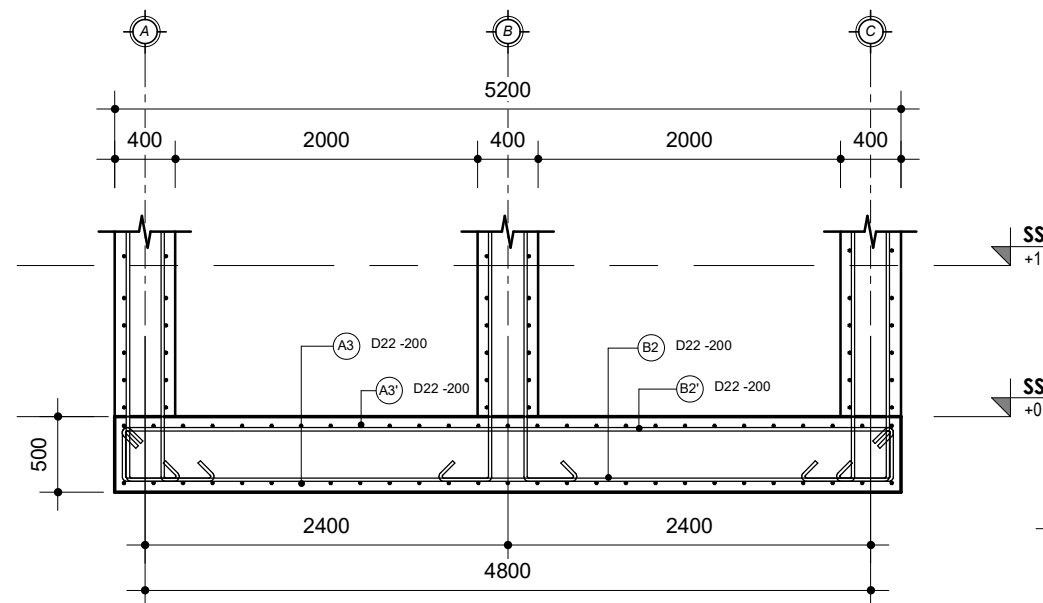

2 Potongan C - Floor Slab
1 : 50

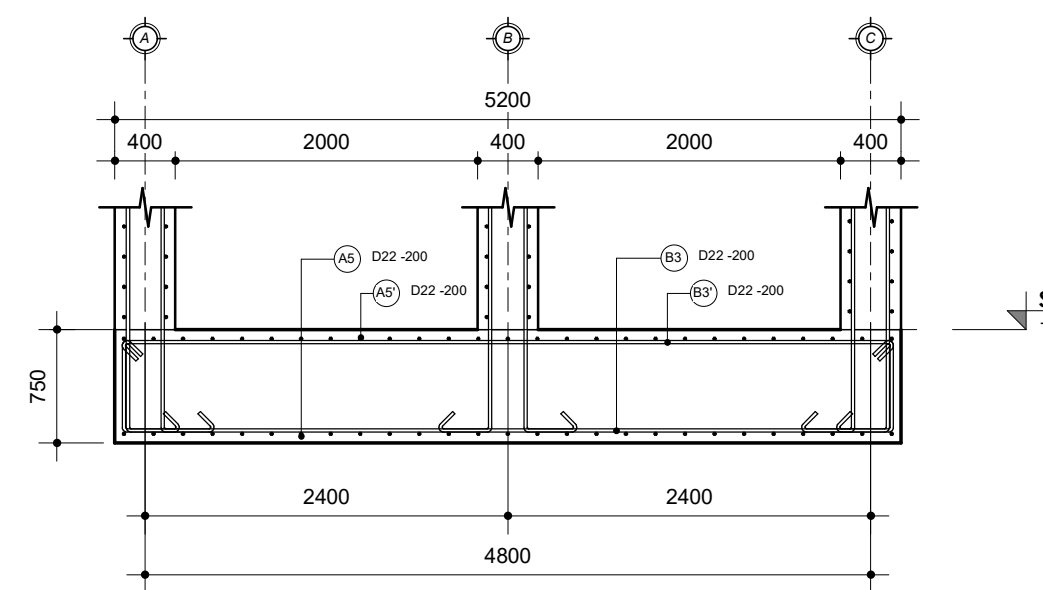

3 Potongan D - Floor Slab
1 : 50

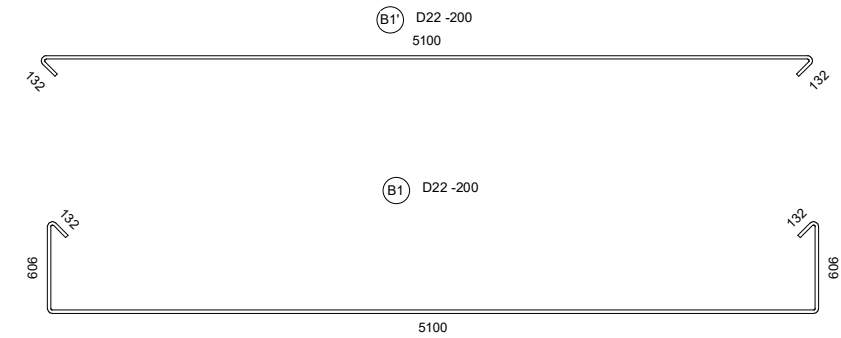

KEMENTERIAN PEKERJAAN UMUM DIREKTORAT JENDERAL SUMBER DAYA AIR BALAI WILAYAH SUNGAI SUMATERA VII BENGKULU SNVT, P.J.S.A., SUMATERA VII, PROVINSI BENGKULU Jl. Sultan Hassanudin No. 25, Bengkulu, 38146				PROVINSI BENGKULU	
PEMBANGUNAN PENGENDALIAN BANJIR AIR BENGKULU KOTA BENGKULU				BWS SUMATERA VII BENGKULU	
CONSTRUCTION DRAWING: PEKERJAAN SLAB KOLAM				Lokasi : Jl. Irian	
DIBUAT OLEH: Manager Proyek Pujiono, ST				Kecamatan : Sungai Serut, Tanjung Agung	
DIPERIKSA DAN DIBETULUHI OLEH: Drafter Yusuf Barakka				Kab./Kota : Kota Bengkulu	
Team Leader Erwin, ST				No. Gambar : S.02.c	
Supervisor Engineer Antonius Ucik, ST				No. Lembar :	
DIREKSI LAPANGAN Franky Antonyo, ST				Tahun : 2025	
				No. Kontrak : HK0102/Bws7.8/272/2025	

SKALA				
	Yang Direvisi	Oleh	Direnc	Diset


Bending Schedule - Slab Kolam					
Mark	Bar Diameter (mm)	Quantity	Bar Length (mm)	DIMENSION	Bending Detail
A1	22	27	12241	A=132 B=650 C=10740 D=650 E=132 F=0	
A1'	22	27	10987	A=10723 B=132 C=132	
A2	22	27	4641	A=115 B=1400 C=840 D=1400 E=865 F=0	
A3	22	27	9301	A=132 B=400 C=8300 D=400 E=132 F=0	
A3'	22	27	8564	A=8300 B=132 C=132	
A4	22	27	3867	A=880 B=2115 C=880 D=0 E=0	
A4'	22	27	4525	A=880 B=2774 C=880 D=0 E=0	
A5	22	27	10542	A=132 B=650 C=9041 D=650 E=132 F=0	
A5'	22	27	9305	A=9041 B=132 C=132	
A6	22	27	3900	A=880 B=1141 C=429 D=1401 E=0 F=132	
A6	22	27	3900	A=880 B=1141 C=429 D=1401 E=0 F=132	
B1	22	55	6513	A=132 B=606 C=5100 D=606 E=132 F=0	
B1	22	1	6438	A=132 B=568 C=5100 D=568 E=132 F=0	
B1	22	1	6750	A=132 B=724 C=5100 D=724 E=132 F=0	
B1	22	1	7062	A=132 B=881 C=5100 D=881 E=132 F=0	

Bending Schedule - Slab Kolam					
Mark	Bar Diameter (mm)	Quantity	Bar Length (mm)	DIMENSION	Bending Detail
B1	22	1	7375	A=132 B=1037 C=5100 D=1037 E=132 F=0	
B1	22	1	6444	A=132 B=572 C=5100 D=572 E=132 F=0	
B1	22	1	6757	A=132 B=728 C=5100 D=728 E=132 F=0	
B1	22	1	7069	A=132 B=884 C=5100 D=884 E=132 F=0	
B1	22	1	7381	A=132 B=1040 C=5100 D=1040 E=132 F=0	
B1'	22	55	5364	A=5100 B=132 C=132	
B1'	22	4	5364	A=5100 B=132 C=132	
B1'	22	4	5364	A=5100 B=132 C=132	
B2	22	43	6013	A=132 B=356 C=5100 D=356 E=132 F=0	
B2'	22	43	5364	A=5100 B=132 C=132	
B3	22	46	6513	A=132 B=606 C=5100 D=606 E=132 F=0	
B3'	22	46	5364	A=5100 B=132 C=132	
B4	22	12	6490	A=132 B=600 C=5089 D=600 E=132 F=0	
B4'	22	14	5364	A=5100 B=132 C=132	
Grand total: 29		627	194762		


SKALA					
-		Yang Direvisi	Oleh	Direnc	Diset

KEMENTERIAN PEKERJAAN UMUM DIREKTORAT JENDERAL SUMBER DAYA AIR BALAI WILAYAH SUNGAI SUMATERA VII BENGKULU SNVT, P.J.S.A., SUMATERA VII PROVINSI BENGKULU Jl. Sungai Serut, Bengkulu, Telp/Fax : (0736) 541405			PROVINSI BENGKULU	
PEMBANGUNAN PENGENDALIAN BANJIR AIR BENGKULU KOTA BENGKULU			BWS SUMATERA VII BENGKULU	
CONSTRUCTION DRAWING:			Lokasi : Jl. Irian	
PEKERJAAN SLAB KOLAM			Kecamatan : Sungai Serut, Tanjung Agung	
DIBUAT OLEH:			Kab./Kota : Kota Bengkulu	
DIPERIKSA DAN DIBETULKAN OLEH:			No. Gambar : S.02.d	
MENGETAHUI:			No. Lembar :	
			Tahun : No. Kontrak	
			2025 HK0102/Bws7.8/272/2025	

Manajer Proyek	Pujiono, ST	
Drafter	Yusuf Barakka	
Team Leader	Erwin, ST	
Supervisor Engineer	Antonius Ucik, ST	
Direksi Lapangan	Franky Antonyo, ST	

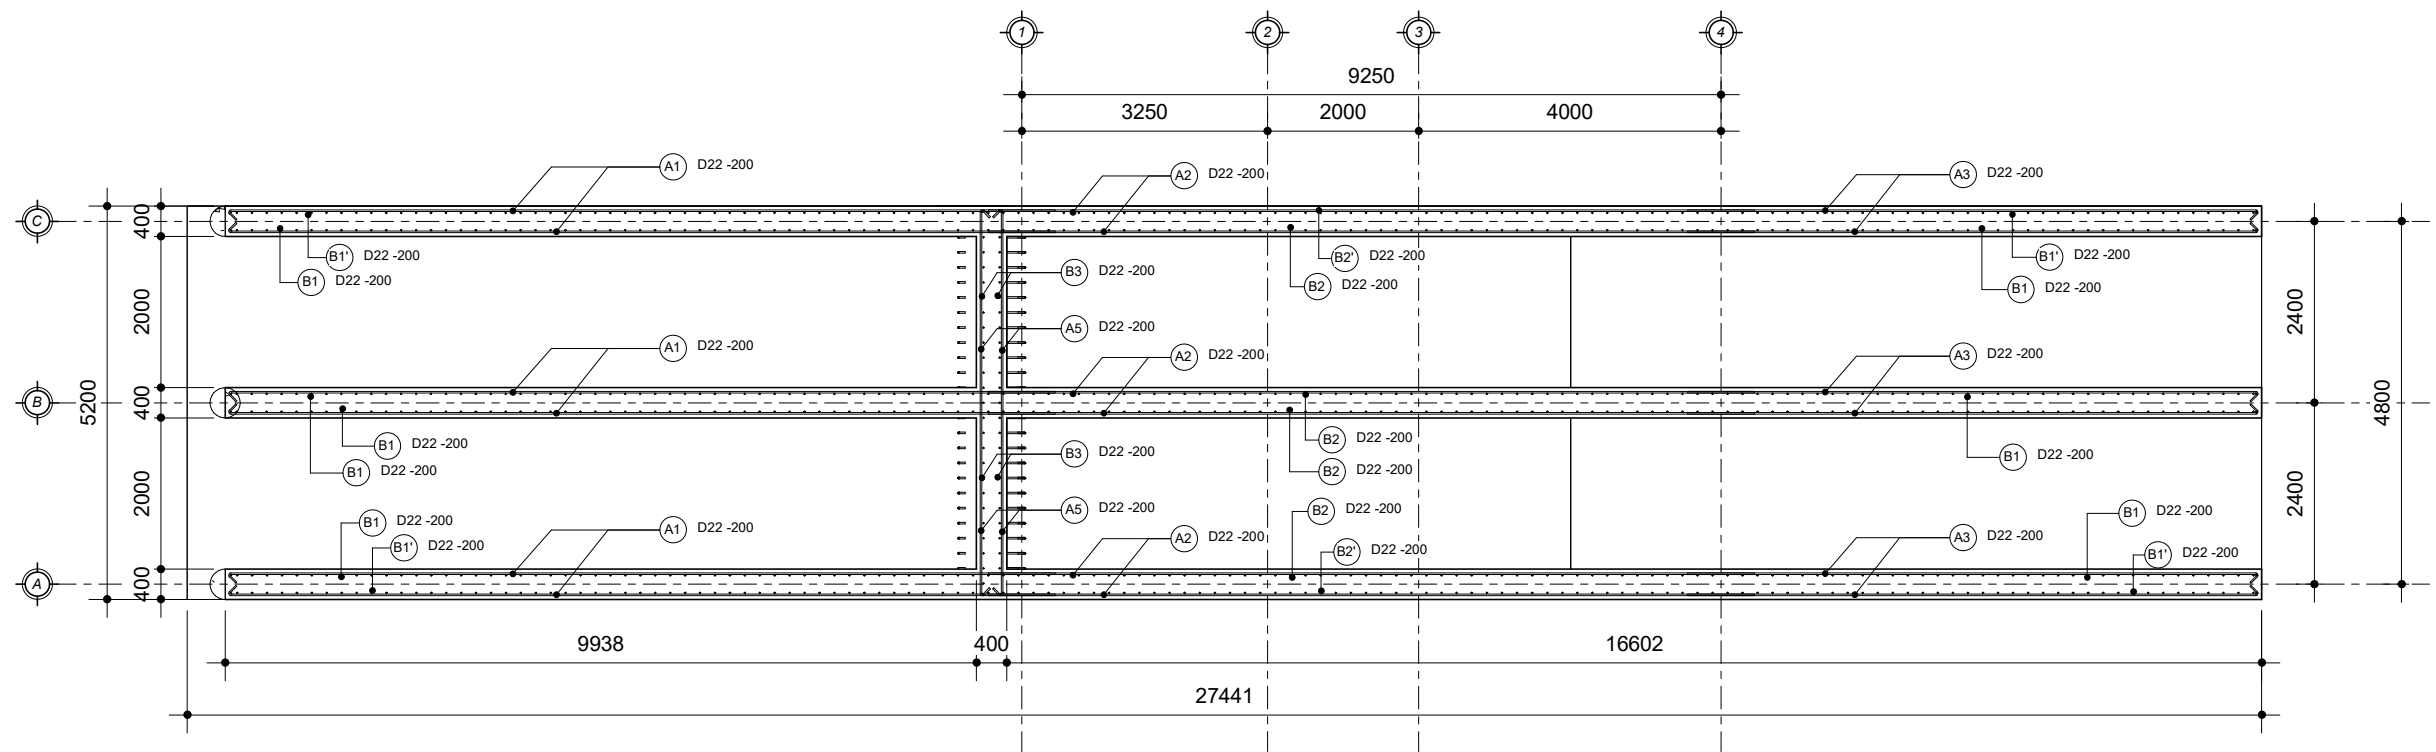

1 Floor Plan - Wall Kolam
1 : 100

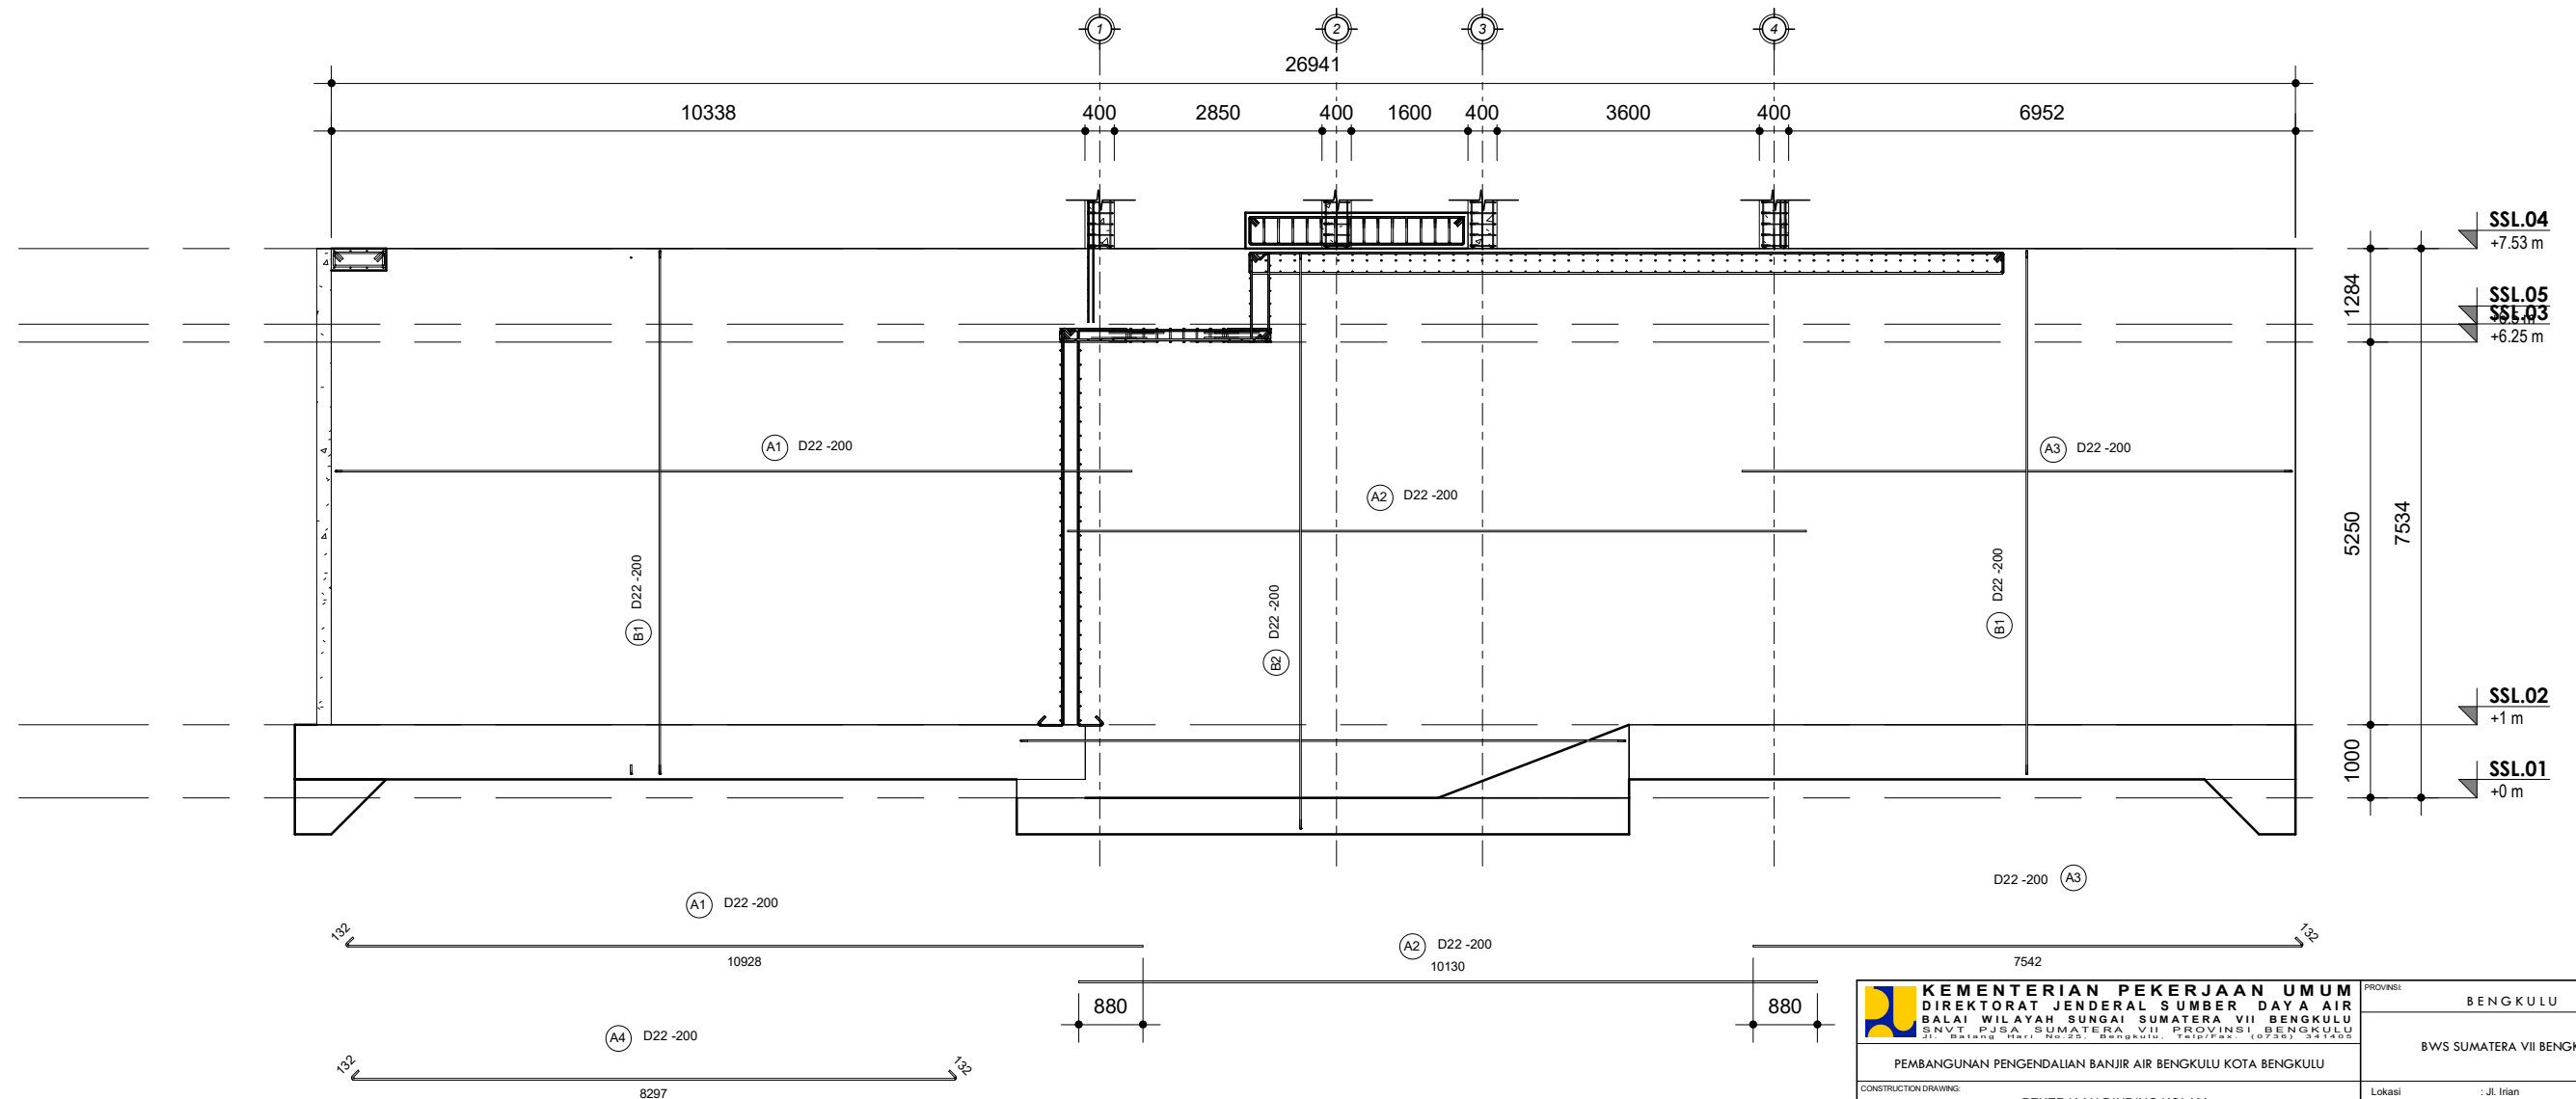


2 Potongan A - Wall Structure
1 : 100



SKALA				Yang Direvisi				Oleh	Direnc	Diset

KEMENTERIAN PEKERJAAN UMUM DIREKTORAT JENDERAL SUMBER DAYA AIR BALAI WILAYAH SUNGAI SUMATERA VII BENGKULU SNVT P.J.S.A., SUMATERA VII PROVINSI BENGKULU Jl. S. R. S. N. No. 22, BENGKULU, Telp/Fax : (0736) 541405				PROVINSI BENGKULU			
PEMBANGUNAN PENGENDALIAN BANJIR AIR BENGKULU KOTA BENGKULU				BWS SUMATERA VII BENGKULU			
CONSTRUCTION DRAWING:				PEKERJAAN DINDING KOLAM			
DIBUAT OLEH:				Lokasi : Jl. Irian			
DIPERIKSA DAN DIBETULUHI OLEH:				Kecamatan : Sungai Serut, Tanjung Agung			
MENGETAHUI:				Kab./Kota : Kota Bengkulu			
				No. Gambar : S.03.b			
				No. Lembar :			
				Tahun		No. Kontrak	
				2025		HK0102/Bws7.8/272/2025	


Manajer Proyek	Pujiono, ST		
Drafter	Yusuf Barakka		
Team Leader	Erwin, ST		
Supervisor Engineer	Antonius Ucik, ST		
Direksi Lapangan	Franky Antonyo, ST		

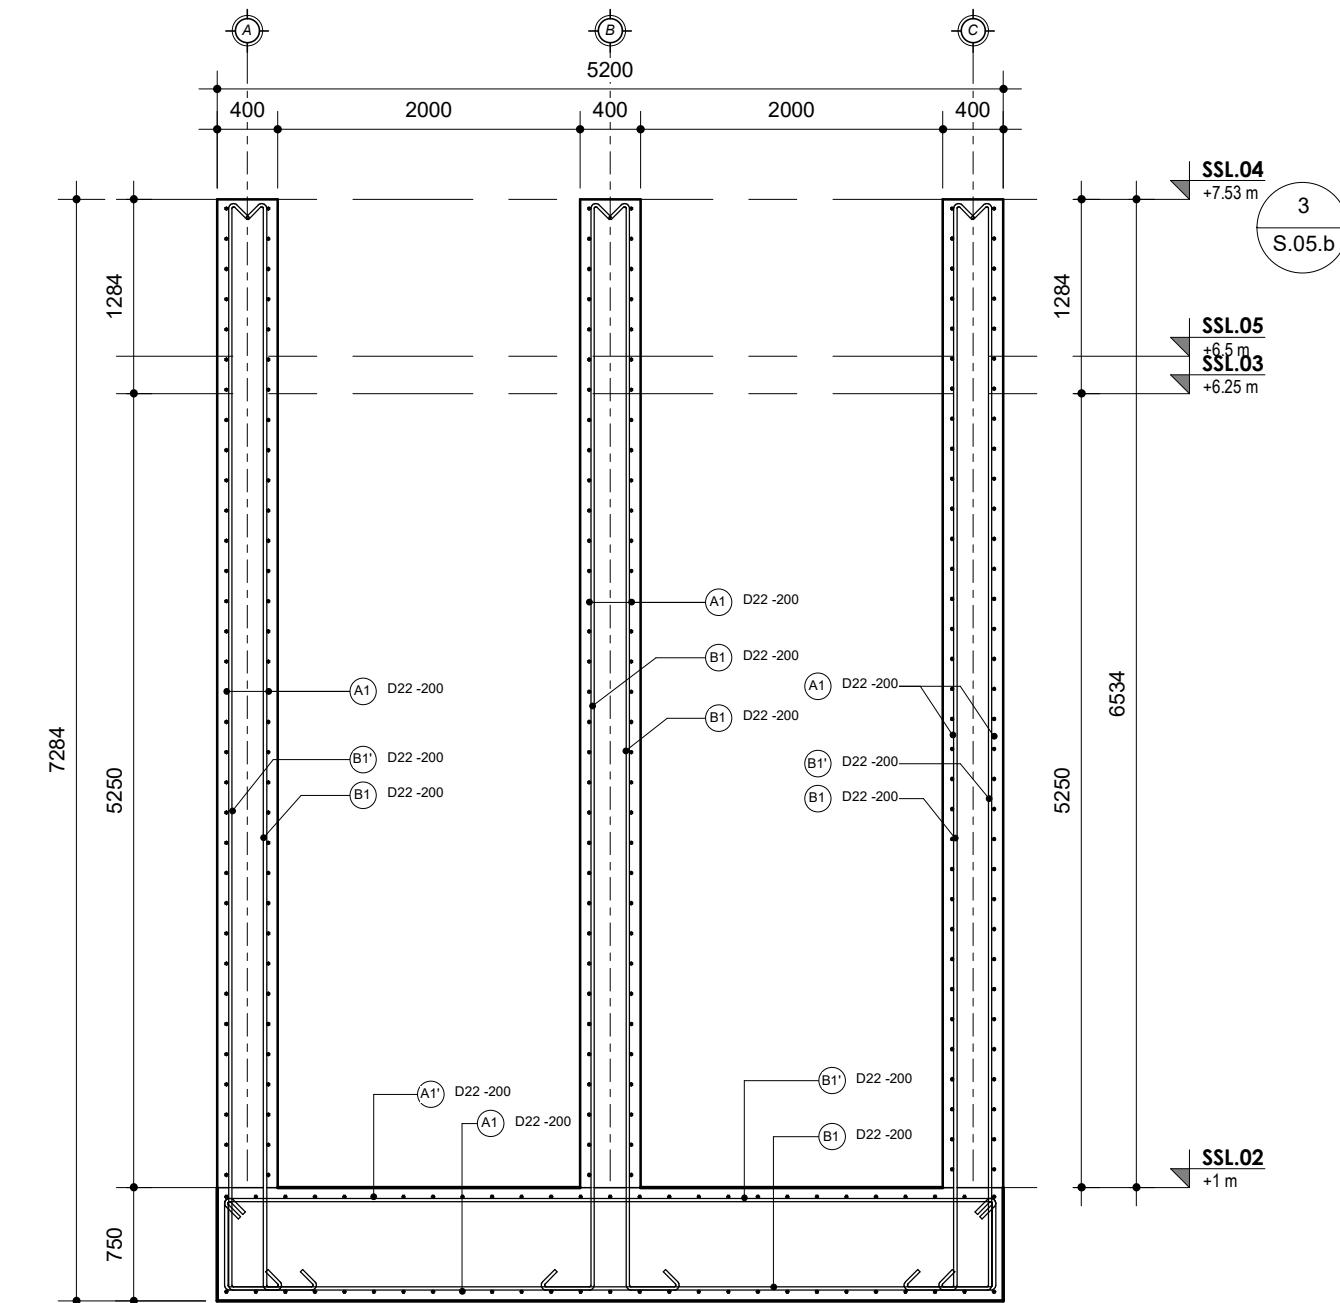

1 Potongan B - Wall Structure
1 : 50

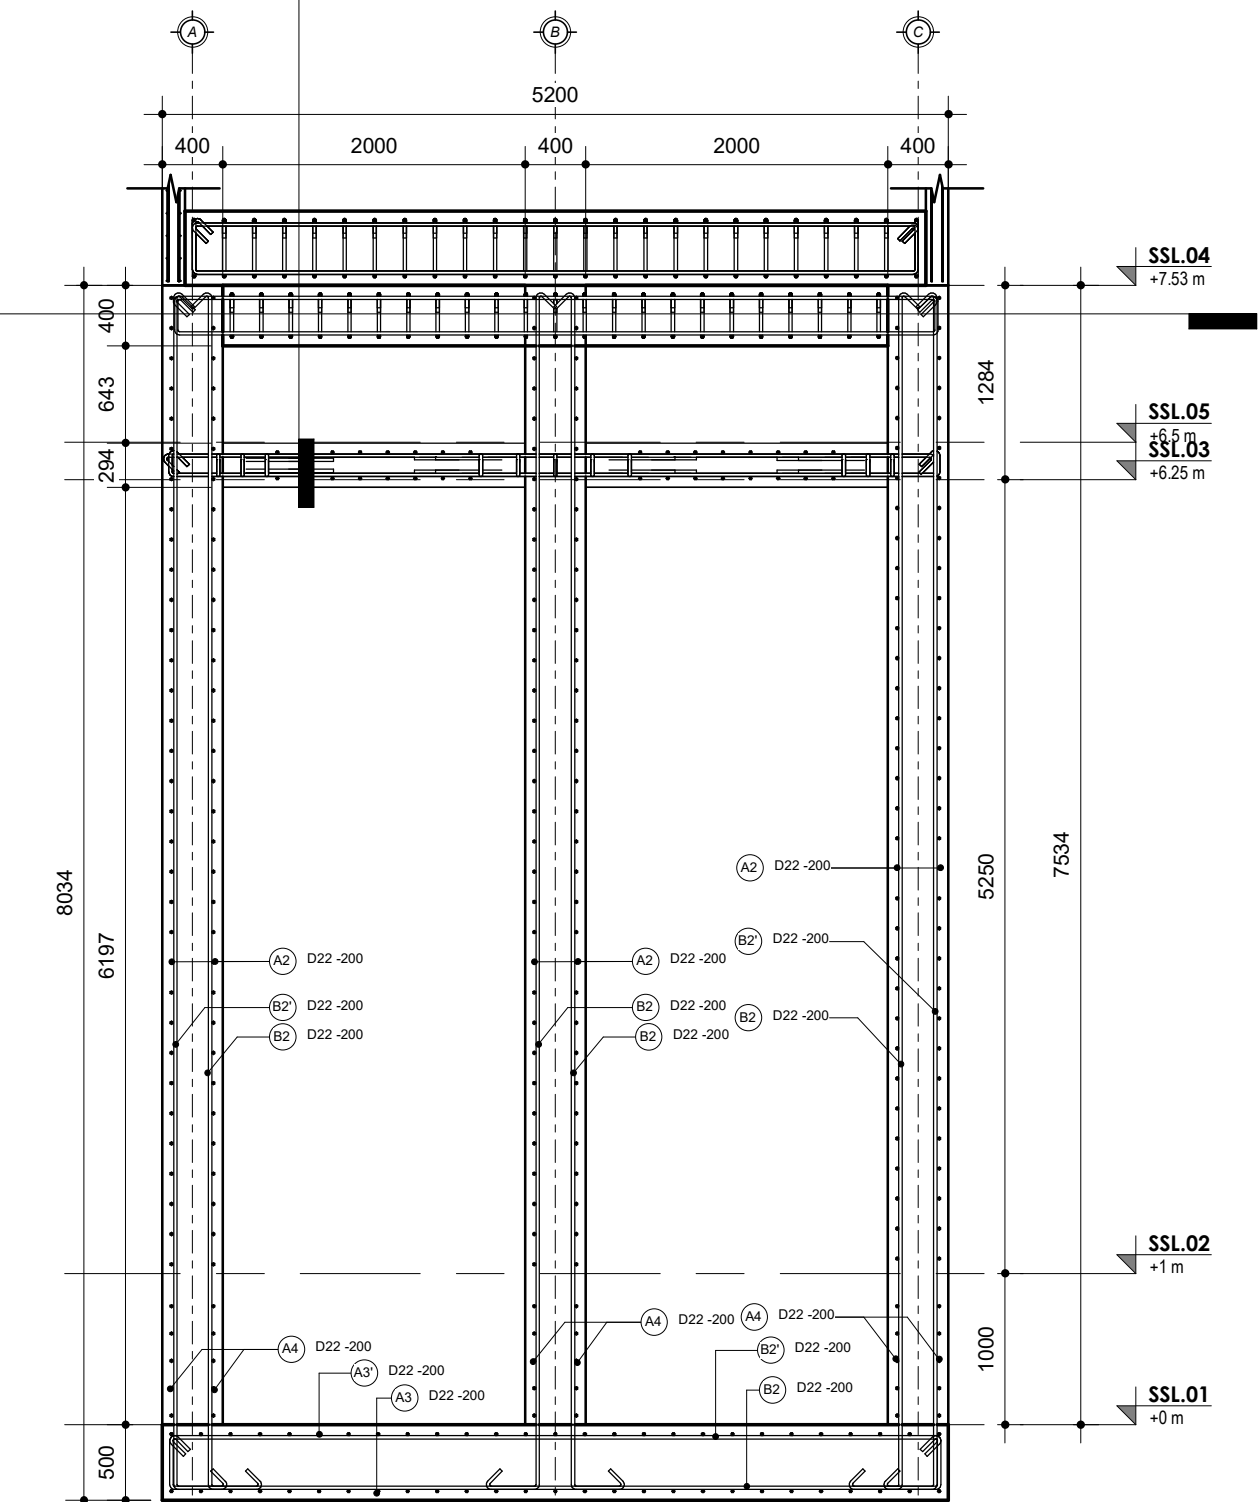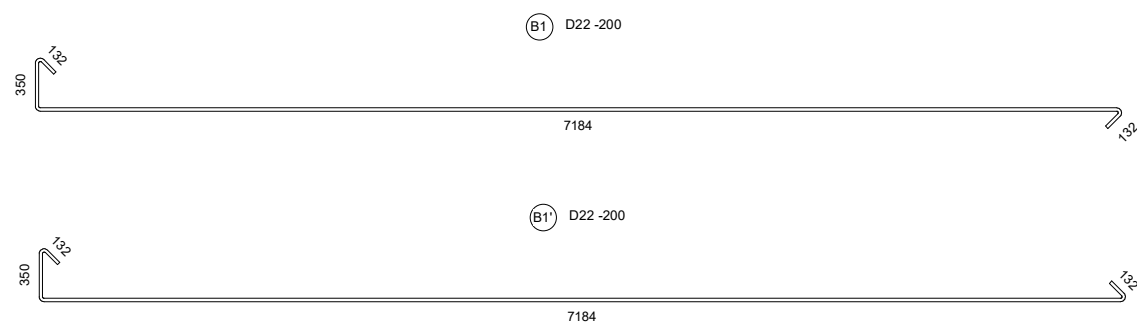

2 Potongan C - Wall Structure
1 : 50

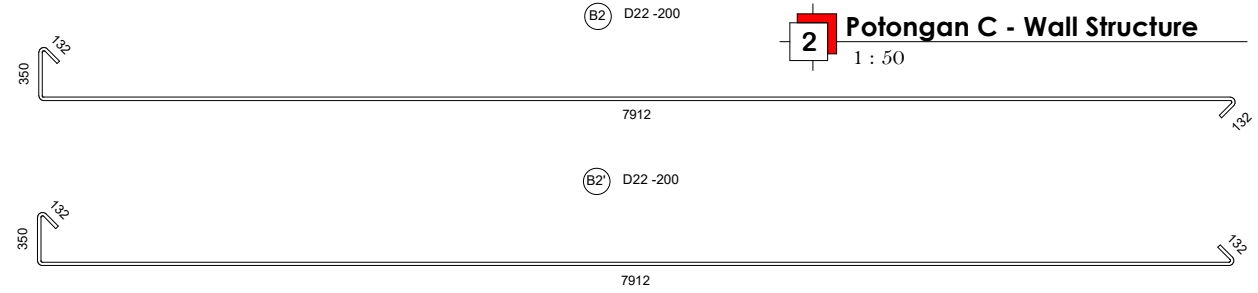

KEMENTERIAN PEKERJAAN UMUM DIREKTORAT JENDERAL SUMBER DAYA AIR BALAI WILAYAH SUNGAI SUMATERA VII BENGKULU SNVT, P.J.S.A., SUMATERA VII PROVINSI BENGKULU Jl. Sungai Serut, Bengkulu, 36100				PROVINSI BENGKULU	
PEMBANGUNAN PENGENDALIAN BANJIR AIR BENGKULU KOTA BENGKULU				BWS SUMATERA VII BENGKULU	
CONSTRUCTION DRAWING: PEKERJAAN DINDING KOLAM				Lokasi : Jl. Irian	
DIBUAT OLEH: Manajer Proyek Pujiono, ST				Kecamatan : Sungai Serut, Tanjung Agung	
DIPERIKSA DAN DIBETULI OLEH: Drafter Yusuf Barakka				Kab./Kota : Kota Bengkulu	
Team Leader Erwin, ST				No. Gambar : S.03.c	
Supervisor Engineer Antonius Ucik, ST				No. Lembar :	
MENGETAHLI: Direksi Lapangan Franky Antonyo, ST				Tahun : 2025	
				No. Kontrak : HK0102/Bws7.8/272/2025	


SKALA				
	Yang Direvisi	Oleh	Direnc	Diset

Wall Structure Rebar Schedule					
Mark	Bar Diameter (mm)	Quantity	Bar Length (mm)	DIMENSION	Bending Detail
	22	46	7767	A=132 B=7184 C=350 D=132 E=0 F=0	
A1	22	33	11060	A=10928 B=0 C=132	
A1	22	33	11060	A=10928 B=0 C=132	
A1	22	33	11060	A=10928 B=0 C=132	
A1	22	33	11060	A=10928 B=0 C=132	
A1	22	33	11060	A=10928 B=0 C=132	
A1	22	33	11060	A=10928 B=0 C=132	
A2	22	33	10130	A=0 B=10130 C=0 D=0 E=0 F=0	
A2	22	33	10130	A=0 B=10130 C=0 D=0 E=0 F=0	
A2	22	33	10130	A=0 B=10130 C=0 D=0 E=0 F=0	
A2	22	33	10130	A=0 B=10130 C=0 D=0 E=0 F=0	
A2	22	33	10130	A=0 B=10130 C=0 D=0 E=0 F=0	
A2	22	33	10130	A=0 B=10130 C=0 D=0 E=0 F=0	
A2	22	33	10130	A=0 B=10130 C=0 D=0 E=0 F=0	
A3	22	33	7674	A=7542 B=0 C=132	
A3	22	33	7674	A=7542 B=0 C=132	
A3	22	33	7674	A=7542 B=0 C=132	
A3	22	33	7674	A=7542 B=0 C=132	
A3	22	33	7674	A=7542 B=0 C=132	
A3	22	33	7674	A=7542 B=0 C=132	
A3	22	33	7674	A=7542 B=0 C=132	
A5	22	27	5364	A=5100 B=132 C=132	
A5	22	27	5364	A=5100 B=132 C=132	


Wall Structure Rebar Schedule					
Mark	Bar Diameter (mm)	Quantity	Bar Length (mm)	DIMENSION	Bending Detail
B1	22	46	7767	A=132 B=7184 C=350 D=132 E=0 F=0	
B1	22	46	7767	A=132 B=7184 C=350 D=132 E=0 F=0	
B1	22	46	7767	A=132 B=7184 C=350 D=132 E=0 F=0	
B1	22	47	7767	A=132 B=7184 C=350 D=132 E=0 F=0	
B1	22	47	7767	A=132 B=7184 C=350 D=132 E=0 F=0	
B1	22	47	7767	A=132 B=7184 C=350 D=132 E=0 F=0	
B1	22	47	7767	A=132 B=7184 C=350 D=132 E=0 F=0	
B1'	22	46	7767	A=132 B=7184 C=350 D=132 E=0 F=0	
B1'	22	46	7768	A=132 B=7187 C=349 D=132 E=0 F=0	
B1'	22	47	7767	A=132 B=7184 C=350 D=132 E=0 F=0	
B1'	22	47	7767	A=132 B=7184 C=350 D=132 E=0 F=0	
B2	22	42	8494	A=132 B=7912 C=350 D=132 E=0 F=0	
B2	22	42	8494	A=132 B=7912 C=350 D=132 E=0 F=0	
B2	22	42	8494	A=132 B=7912 C=350 D=132 E=0 F=0	
B2	22	42	8494	A=132 B=7912 C=350 D=132 E=0 F=0	
B2'	22	42	8494	A=132 B=7912 C=350 D=132 E=0 F=0	
B2'	22	42	8494	A=132 B=7912 C=350 D=132 E=0 F=0	
B3	22	23	6038	A=132 B=5456 C=350 D=132 E=0 F=0	
B3	22	24	6038	A=132 B=5456 C=350 D=132 E=0 F=0	
Grand total: 40		1505	340160		

 KEMENTERIAN PEKERJAAN UMUM DIREKTORAT JENDERAL SUMBER DAYA AIR BALAI WILAYAH SUNGAI SUMATERA VII BENGKULU SNVT, P.J.S.A., SUMATERA VII PROVINSI BENGKULU Jl. Sungai Serut, Tanjung Agung, Kota Bengkulu 36123				PROVINSI BENGKULU	
PEMBANGUNAN PENGENDALIAN BANJIR AIR BENGKULU KOTA BENGKULU				BWS SUMATERA VII BENGKULU	
CONSTRUCTION DRAWING: PEKERJAAN DINDING KOLAM				Lokasi : Jl. Irian	
DIBUAT OLEH: Manajer Proyek Pujiono, ST				Kecamatan : Sungai Serut, Tanjung Agung	
DRAFTER: Yusuf Barakka				Kab./Kota : Kota Bengkulu	
DIPERIKSA DAN DIBETULI OLEH: Team Leader Erwin, ST				No. Gambar : S.03.d	
SUPERVISOR ENGINEER: Antonius Ucik, ST				No. Lembar :	
MENGETAHI: Direksi Lapangan Franky Antonyo, ST				Tahun : 2025	
				No. Kontrak : HK0102/Bws7.8/272/2025	


SKALA				
	Yang Direvisi	Oleh	Direnc	Diset

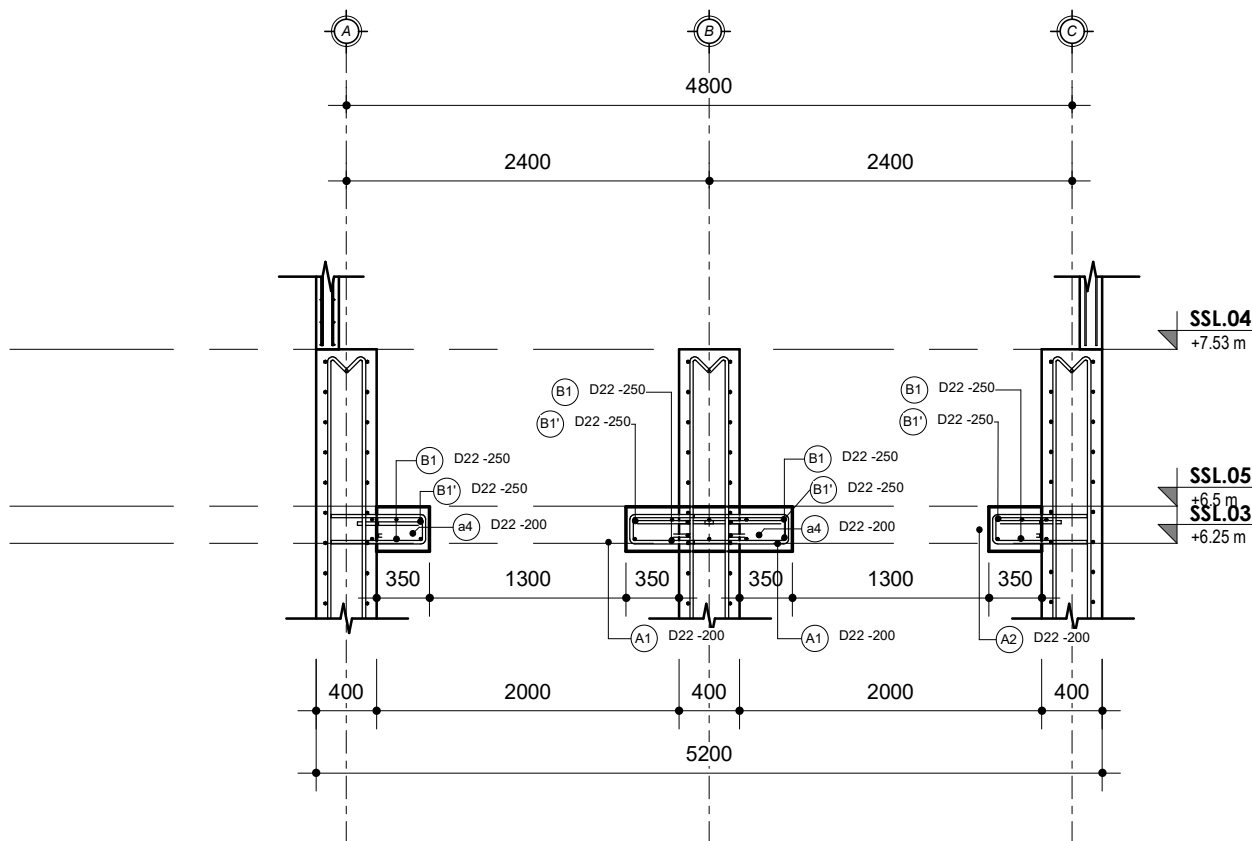


1 Potongan C - Slab pompa
1 : 50

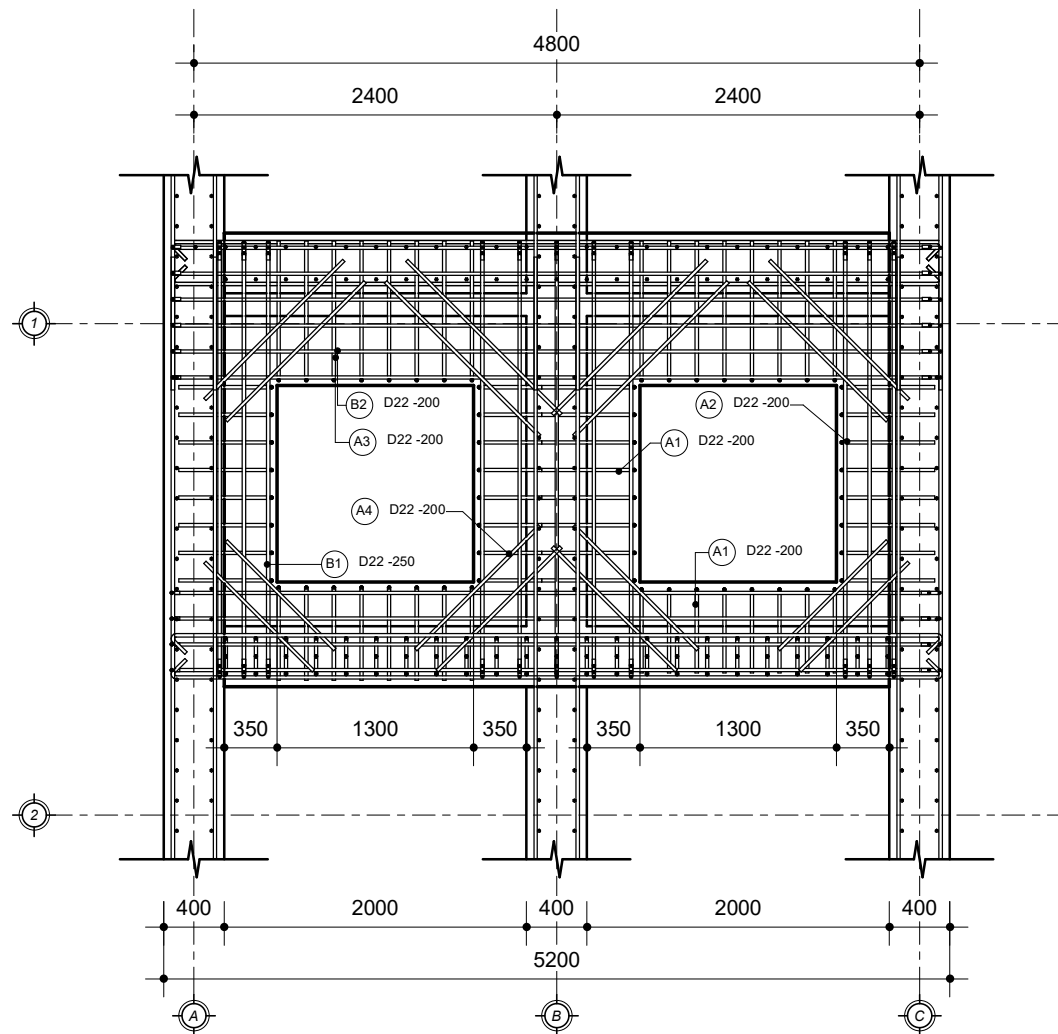

3 Plan View - Slab Pompa
1 : 50

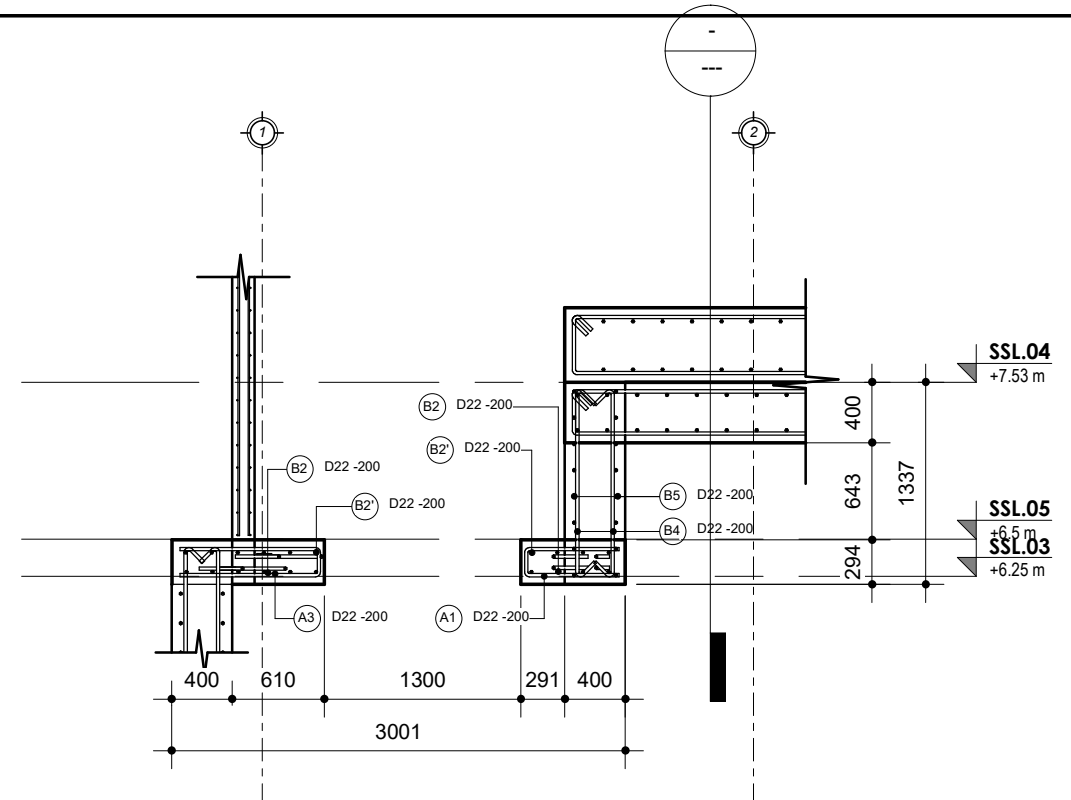

2 Potongan A - Slab Pompa
1 : 50

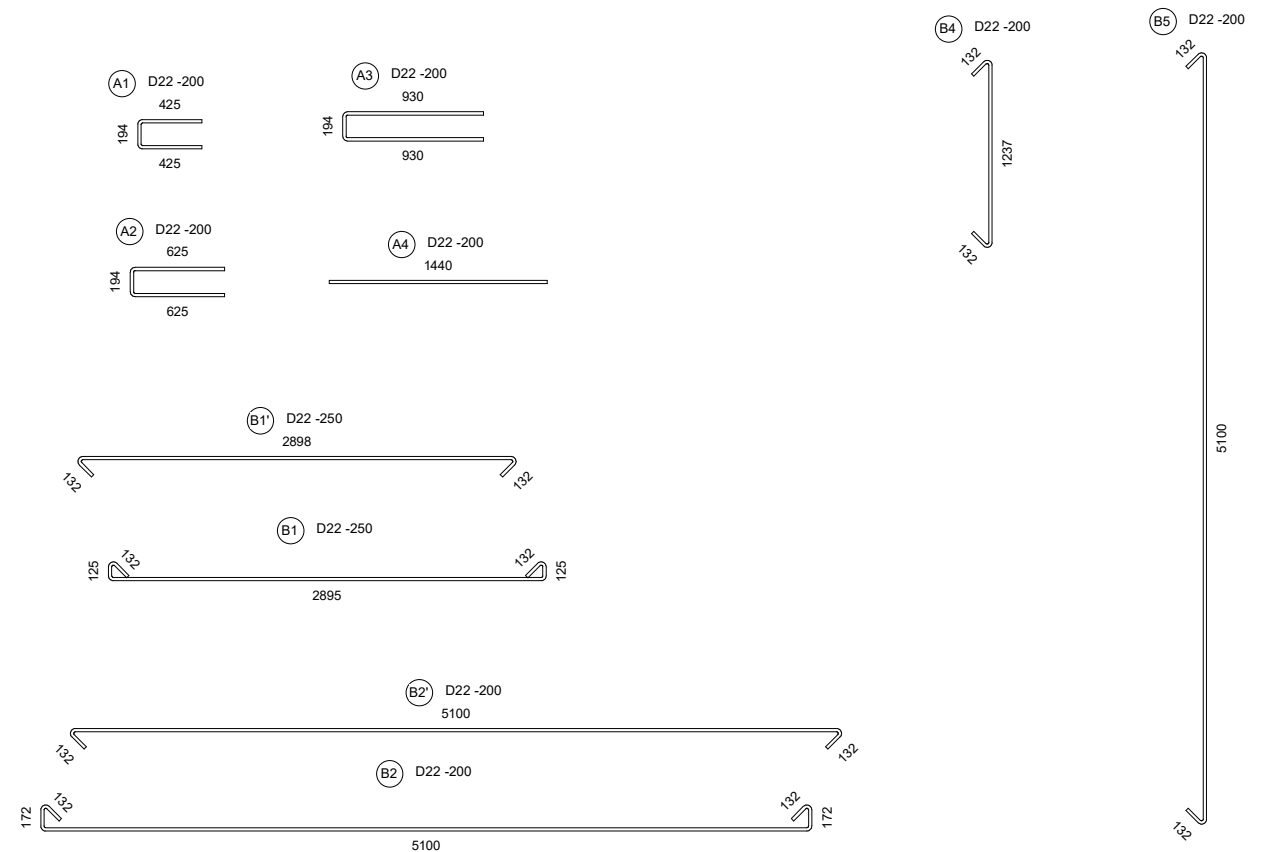

KEMENTERIAN PEKERJAAN UMUM DIREKTORAT JENDERAL SUMBER DAYA AIR BALAI WILAYAH SUNGAI SUMATERA VII BENGKULU SNVT PJSB, SUMATERA VII PROVINSI BENGKULU Jl. S. R. M. No. 25, Bengkulu, Telp/Fax : (0736) 541405				PROVINSI BENGKULU	
PEMBANGUNAN PENGENDALIAN BANJIR AIR BENGKULU KOTA BENGKULU				BWS SUMATERA VII BENGKULU	
CONSTRUCTION DRAWING: PEKERJAAN SLAB POMPA				Lokasi : Jl. Irian	
DIBUAT OLEH: Manager Proyek Pujiono, ST				Kecamatan : Sungai Serut, Tanjung Agung	
DIPERIKSA DAN DIBETULI OLEH: Drafter Yusuf Barakka				Kab./Kota : Kota Bengkulu	
Team Leader Erwin, ST				No. Gambar : S.04.b	
Supervisor Engineer Antonius Ucik, ST				No. Lembar :	
MENGETAHUI: Direksi Lapangan Franky Antonyo, ST				Tahun : 2025	
				No. Kontrak : HK0102/Bws7.8/272/2025	


SKALA					
	Yang Direvisi	Oleh	Direnc	Diset	

Bending Schedule - Slab Pompa					
Mark	Bar Diameter (mm)	Quantity	Bar Length (mm)	DIMENSION	Bending Detail
A1	22	8	981	A=425 B=194 C=425 D=0 E=0	
A1	22	8	1381	A=625 B=194 C=625 D=0 E=0	
A1	22	8	1381	A=625 B=194 C=625 D=0 E=0	
A1	22	8	1256	A=562 B=194 C=562 D=0 E=0	
A2	22	8	1381	A=625 B=194 C=625 D=0 E=0	
A2	22	8	1381	A=625 B=194 C=625 D=0 E=0	
A3	22	8	1991	A=930 B=194 C=930 D=0 E=0	
A3	22	8	1991	A=930 B=194 C=930 D=0 E=0	
A4	22	2	1299	A=0 B=1299 C=0 D=0 E=0 F=0	
A4	22	2	1440	A=0 B=1440 C=0 D=0 E=0 F=0	
A4	22	2	1016	A=0 B=1016 C=0 D=0 E=0 F=0	
A4	22	2	1016	A=0 B=1016 C=0 D=0 E=0 F=0	
A4	22	2	1158	A=0 B=1158 C=0 D=0 E=0 F=0	
A4	22	2	1440	A=0 B=1440 C=0 D=0 E=0 F=0	
A4	22	2	1299	A=0 B=1299 C=0 D=0 E=0 F=0	
a4	22	2	1299	A=0 B=1299 C=0 D=0 E=0 F=0	
a4	22	2	1158	A=0 B=1158 C=0 D=0 E=0 F=0	
a4	22	2	1440	A=0 B=1440 C=0 D=0 E=0 F=0	
a4	22	2	1440	A=0 B=1440 C=0 D=0 E=0 F=0	
a4	22	2	1016	A=0 B=1016 C=0 D=0 E=0 F=0	
a4	22	2	1299	A=0 B=1299 C=0 D=0 E=0 F=0	


Bending Schedule - Slab Pompa					
Mark	Bar Diameter (mm)	Quantity	Bar Length (mm)	DIMENSION	Bending Detail
B1	22	5	3346	A=132 B=125 C=2895 D=125 E=132 F=0	
B1	22	3	3346	A=132 B=125 C=2895 D=125 E=132 F=0	
B1	22	3	3346	A=132 B=125 C=2895 D=125 E=132 F=0	
B1'	22	5	3162	A=2898 B=132 C=132	
B1'	22	3	3162	A=2898 B=132 C=132	
B1'	22	3	3162	A=2898 B=132 C=132	
B2	22	6	5645	A=132 B=172 C=5100 D=172 E=132 F=0	
B2	22	4	5645	A=132 B=172 C=5100 D=172 E=132 F=0	
B2'	22	6	5364	A=5100 B=132 C=132	
B2'	22	4	5364	A=5100 B=132 C=132	
B4	22	23	1501	A=1237 B=132 C=132	
B4	22	23	1501	A=1237 B=132 C=132	
B5	22	8	5364	A=5100 B=132 C=132	
B5	22	8	5364	A=5100 B=132 C=132	
Grand total: 35		194	83338		

SKALA				
	Yang Direvisi	Oleh	Direnc	Diset


 KEMENTERIAN PEKERJAAN UMUM DIREKTORAT JENDERAL SUMBER DAYA AIR BALAI WILAYAH SUNGAI SUMATERA VII BENGKULU SNVT PJSB SUMATERA VII PROVINSI BENGKULU Jl. Sungai Serut, Bengkulu, 36140 Telp/Fax : (0736) 541405				PROVINSI BENGKULU	
PEMBANGUNAN PENGENDALIAN BANJIR AIR BENGKULU KOTA BENGKULU				BWS SUMATERA VII BENGKULU	
CONSTRUCTION DRAWING:				Lokasi : Jl. Irian	
PEKERJAAN SLAB POMPA				Kecamatan : Sungai Serut, Tanjung Agung	
DIBUAT OLEH:		Manajer Proyek	Pujiono, ST	Kab./Kota : Kota Bengkulu	
DIPERIKSA DAN DIBETULUHOleh:		Drafter	Yusuf Barakka	No. Gambar : S.04.c	
		Team Leader	Erwin, ST	No. Lembar :	
		Supervisor Engineer	Antonius Ucik, ST	Tahun : No. Kontrak	
MENGETAHUI:		Direksi Lapangan	Franky Antonyo, ST	2025 HK0102/Bws7.8/272/2025	

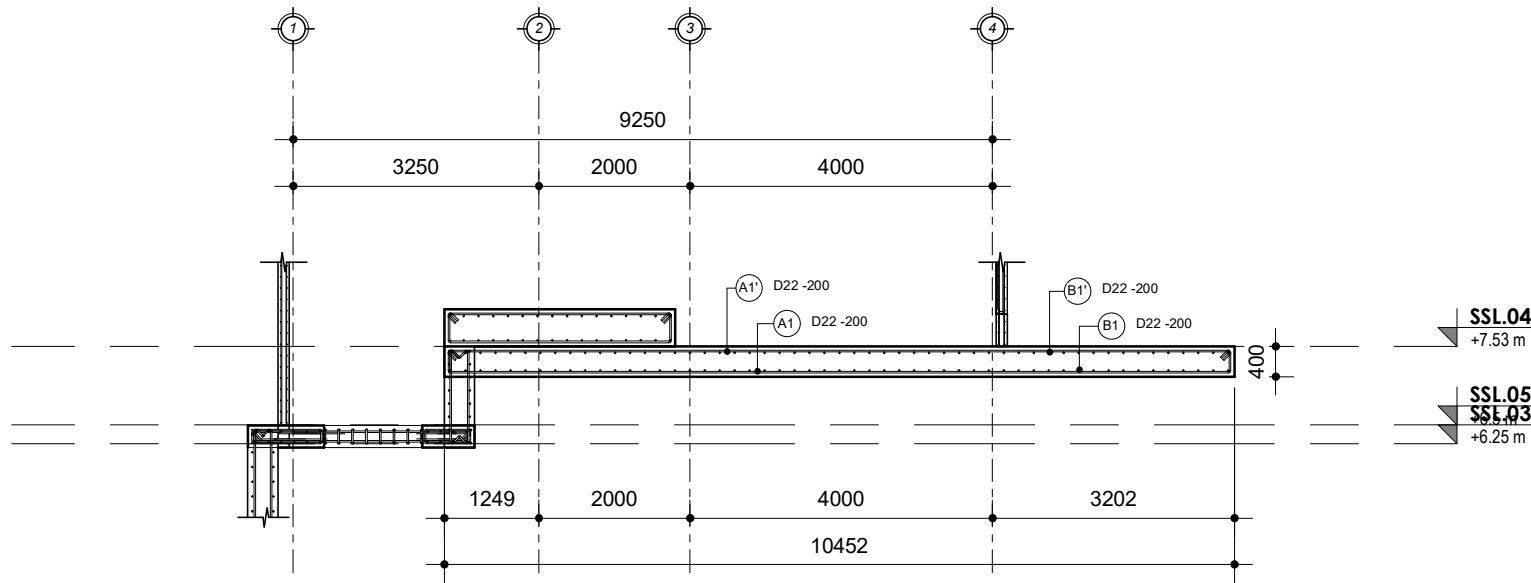


1 Potongan A - Slab Lantai
1 : 100

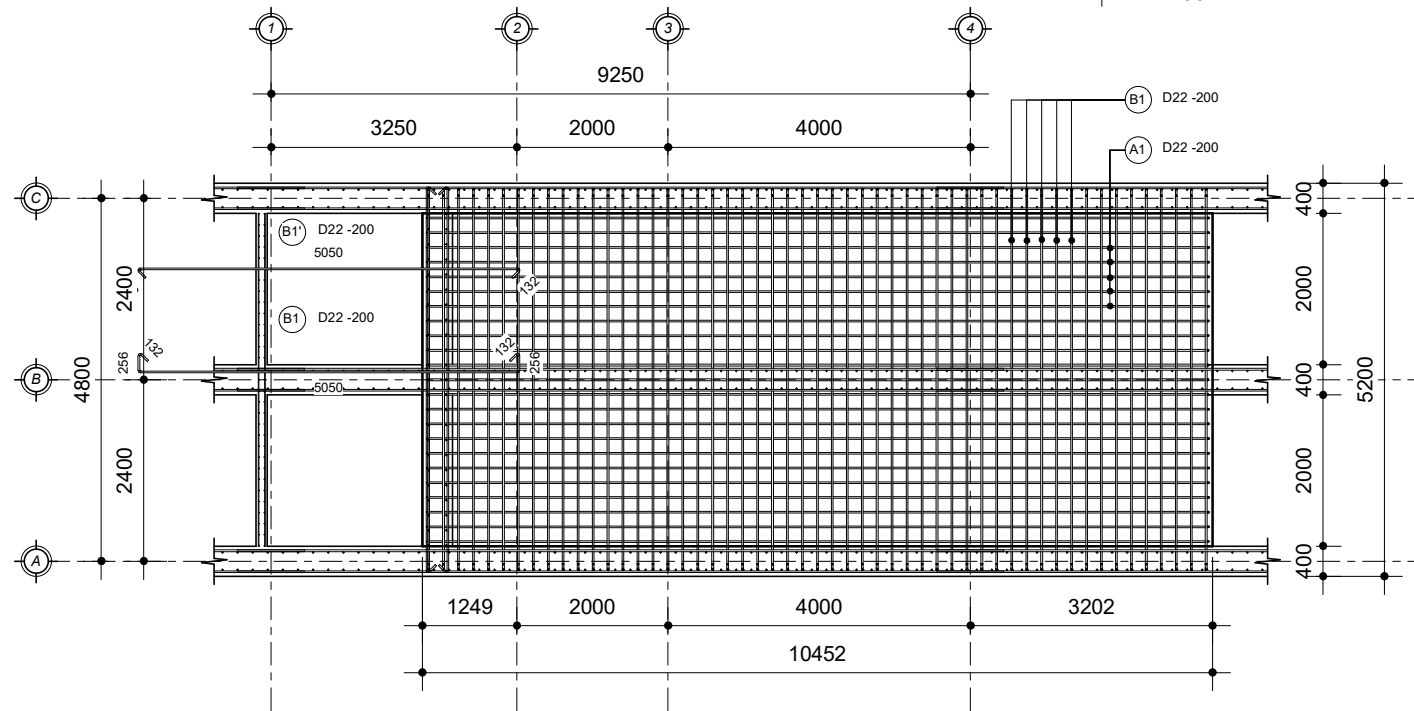

3 Floor Plan - Slab Lantai
1 : 100

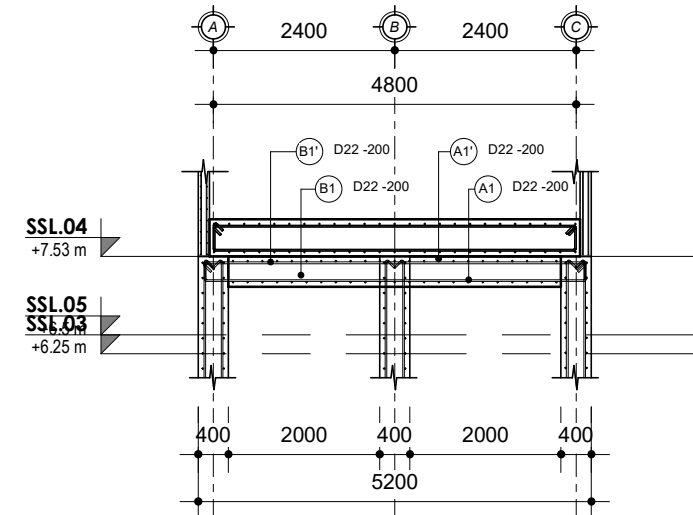


2 Potongan C - Slab Lantai
1 : 100

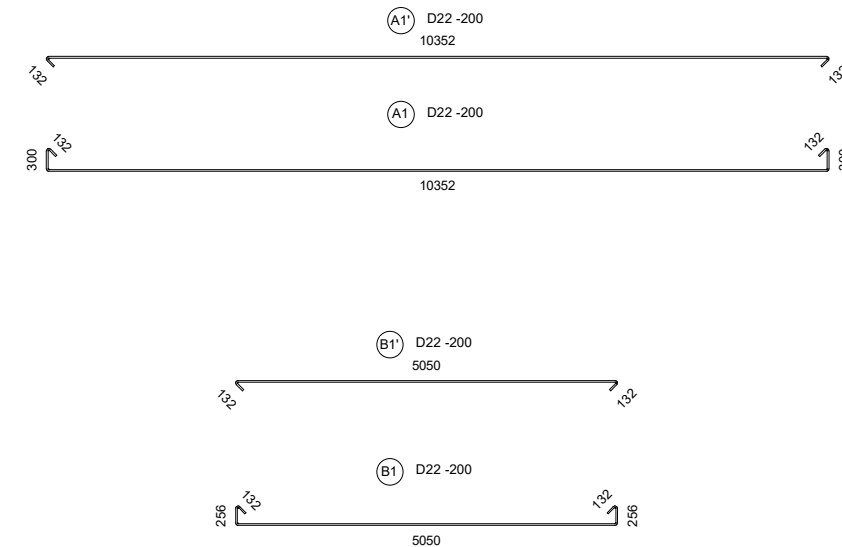

KEMENTERIAN PEKERJAAN UMUM DIREKTORAT JENDERAL SUMBER DAYA AIR BALAI WILAYAH SUNGAI SUMATERA VII BENGKULU SNVT, P.J.S.A., SUMATERA VII, PROVINSI BENGKULU Jl. Sungai Serut, Bengkulu, Telp/Fax: (0736) 541405				PROVINSI BENGKULU	
PEMBANGUNAN PENGENDALIAN BANJIR AIR BENGKULU KOTA BENGKULU				BWS SUMATERA VII BENGKULU	
CONSTRUCTION DRAWING: PEKERJAAN SLAB LANTAI				Lokasi : Jl. Irian	
DIBUAT OLEH: Manager Proyek Pujiono, ST				Kecamatan : Sungai Serut, Tanjung Agung	
DIPERIKSA DAN DIBETULI OLEH: Drafter Yusuf Barakka				Kab./Kota : Kota Bengkulu	
Team Leader Erwin, ST				No. Gambar : S.05.b	
Supervisor Engineer Antonius Ucik, ST				No. Lembar :	
MENGETAHUI: Direksi Lapangan Franky Antonyo, ST				Tahun : 2025	No. Kontrak : HK0102/Bws7.8/272/2025


SKALA				
	Yang Direvisi	Oleh	Direnc	Diset

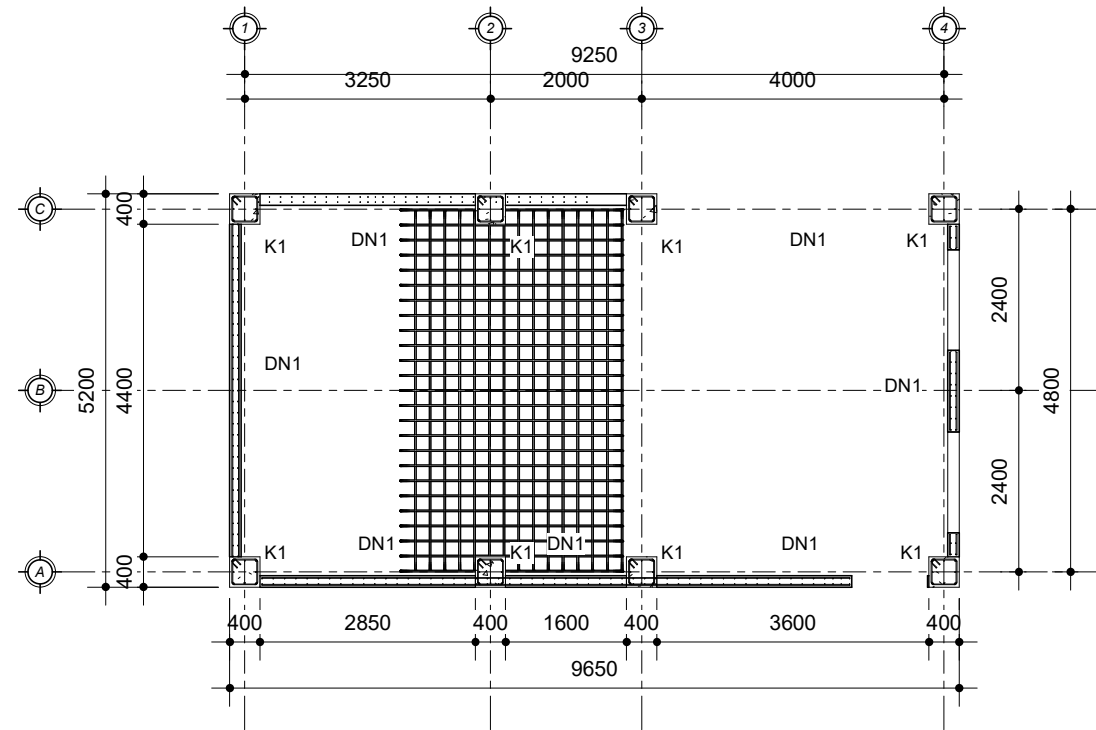

1 Floor Plan - Column
1 : 100

SKALA				
	Yang Direvisi	Oleh	Direnc	Diset


 KEMENTERIAN PEKERJAAN UMUM DIREKTORAT JENDERAL SUMBER DAYA AIR BALAI WILAYAH SUNGAI SUMATERA VII BENGKULU SNVT, PJSB, SUMATERA VII, PROVINSI BENGKULU Jl. Sungai Serut, Kota Bengkulu, Telp/Fax: (0736) 541405			PROVINSI BENGKULU	
			BWS SUMATERA VII BENGKULU	
PEMBANGUNAN PENGENDALIAN BANJIR AIR BENGKULU KOTA BENGKULU			Lokasi : Jl. Irian	
CONSTRUCTION DRAWING: PEKERJAAN KOLOM DAN DINDING			Kecamatan : Sungai Serut, Tanjung Agung	
DIBUAT OLEH:			Kab./Kota : Kota Bengkulu	
DIPERIKSA DAN DIBETULUI OLEH:			No. Gambar : S.06.b	
MENGETAHUI:			No. Lembar :	
			Tahun	No. Kontrak
			2025	HK0102/Bws7.8/272/2025

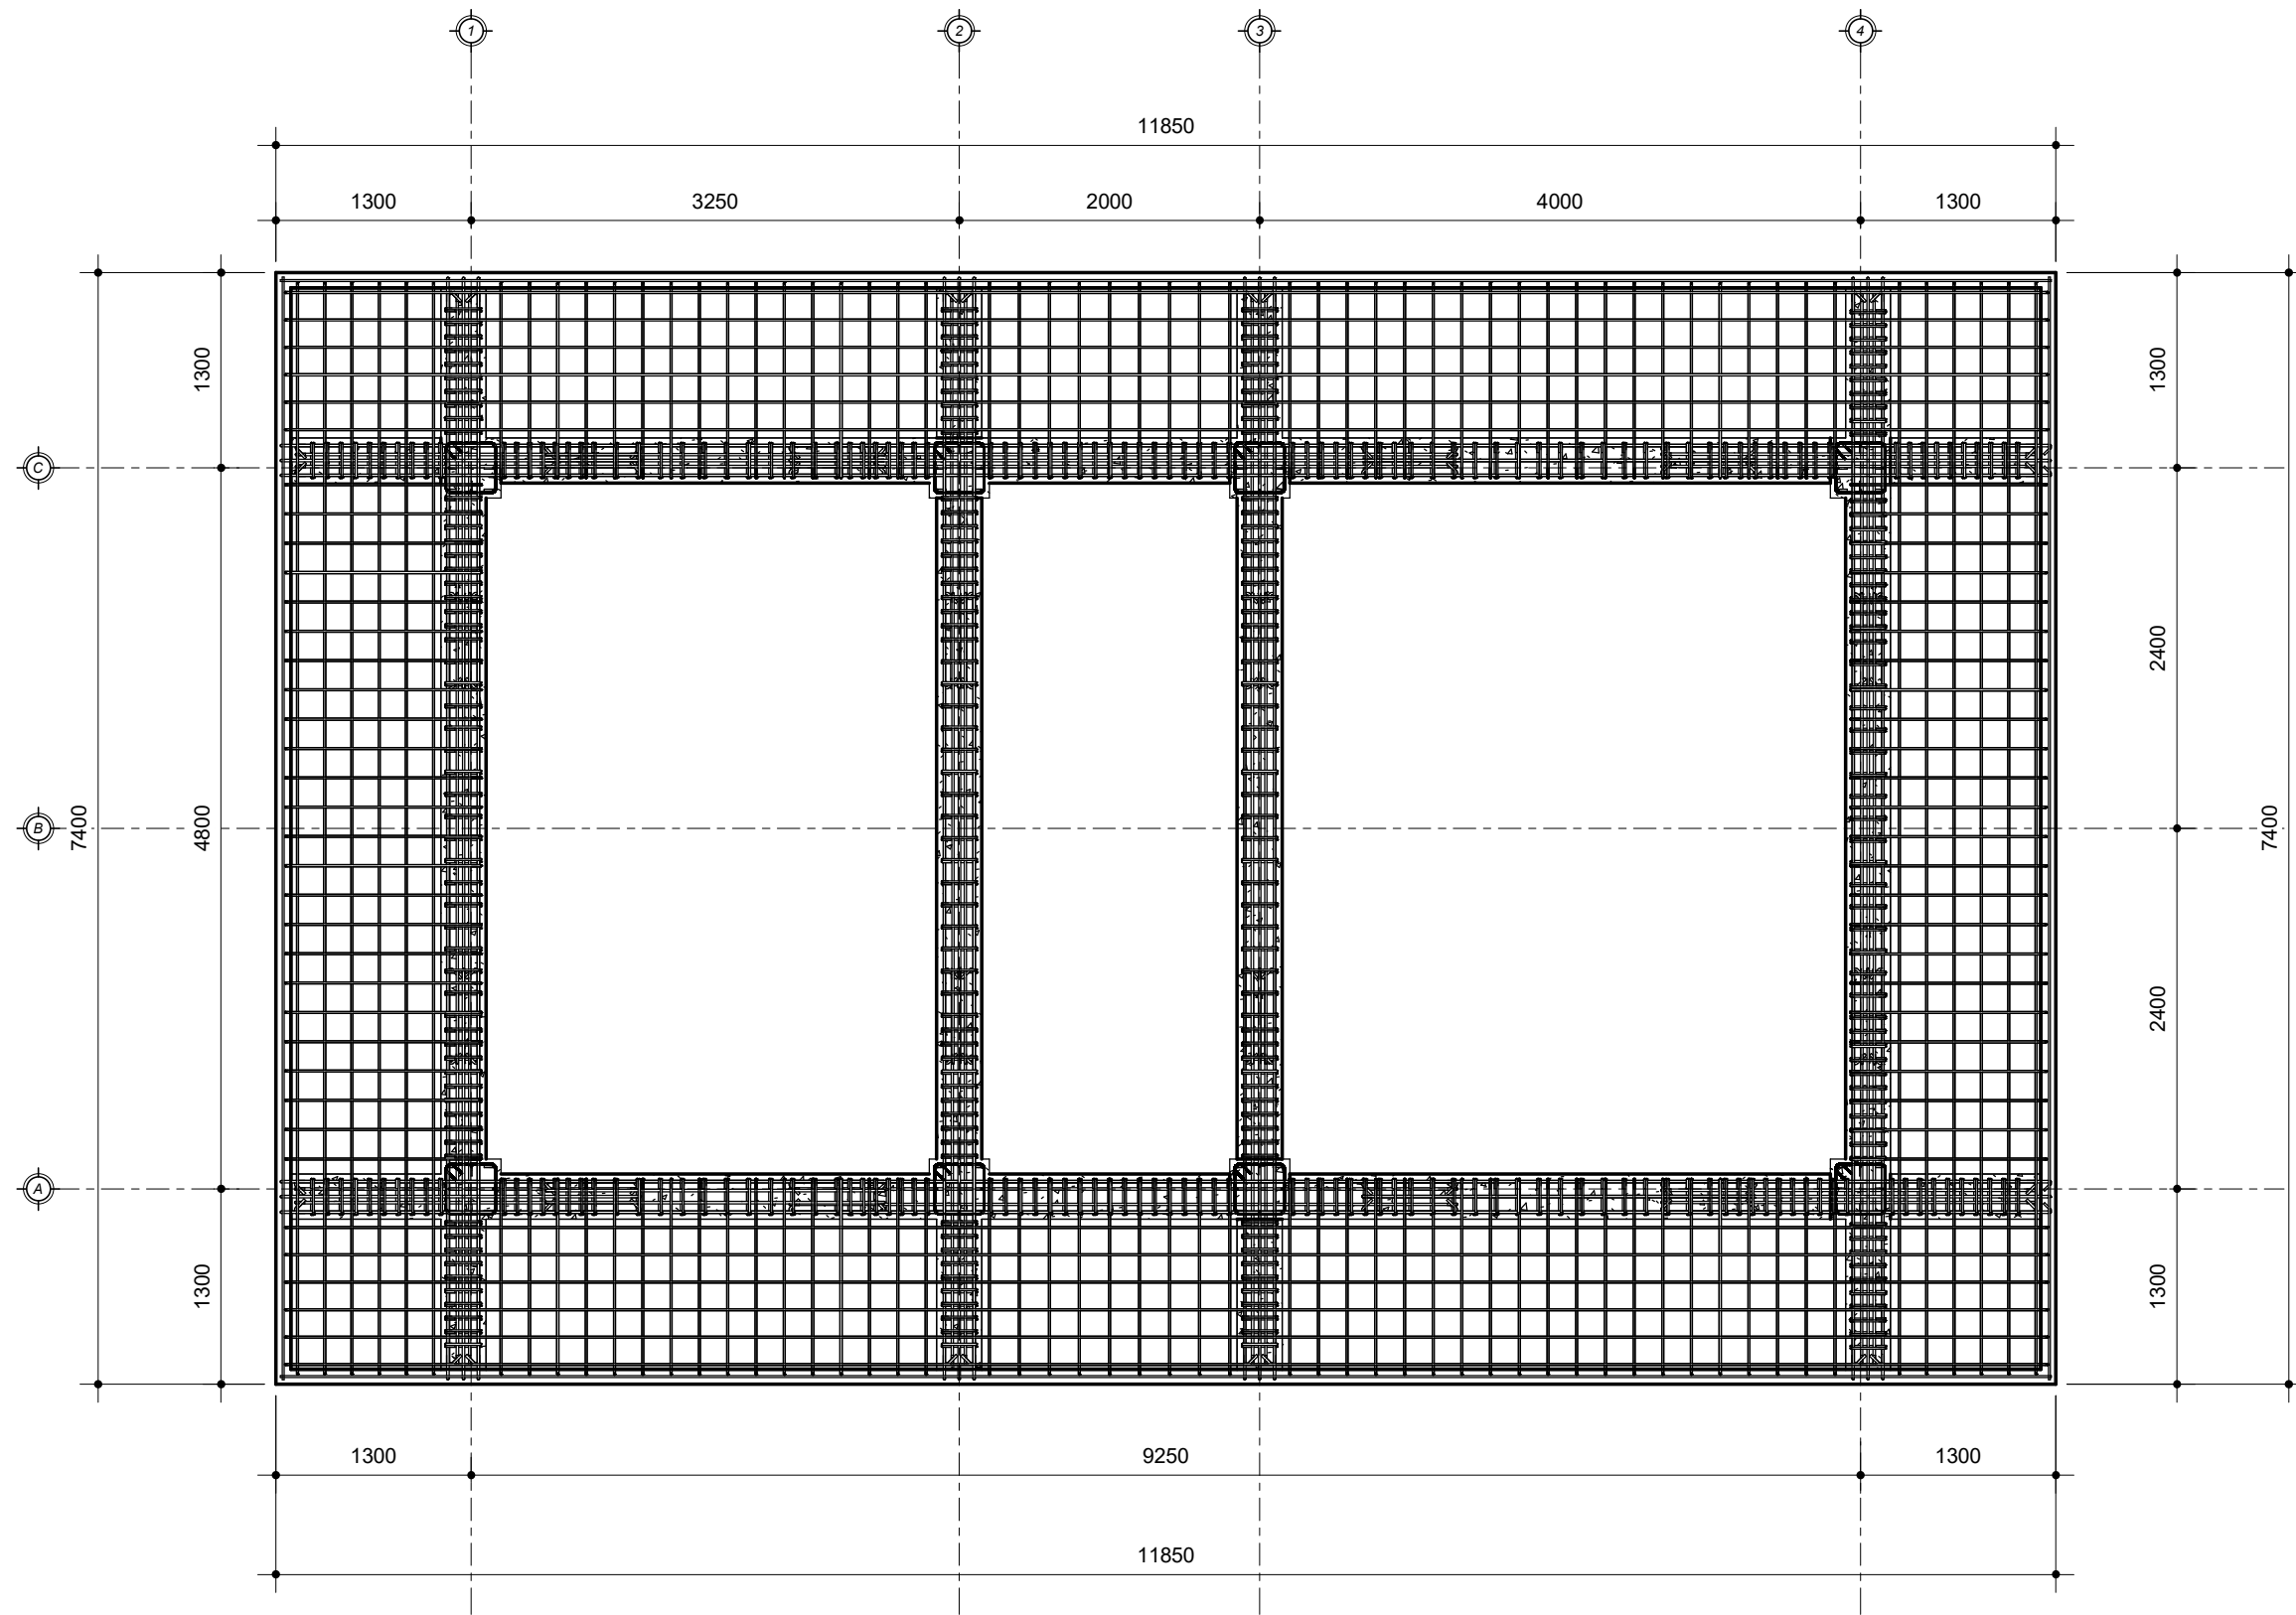


1 Floor Plan - Slab Atas
1 : 50

SKALA				
	Yang Direvisi	Oleh	Direnc	Diset


 KEMENTERIAN PEKERJAAN UMUM DIREKTORAT JENDERAL SUMBER DAYA AIR BALAI WILAYAH SUNGAI SUMATERA VII BENGKULU SNVT PJSB SUMATERA VII PROVINSI BENGKULU Jl. Sungai Serut, Kota Bengkulu, Telp/Fax : (0736) 541405			PROVINSI BENGKULU	
			BWS SUMATERA VII BENGKULU	
PEMBANGUNAN PENGENDALIAN BANJIR AIR BENGKULU KOTA BENGKULU			Lokasi : Jl. Irian	
CONSTRUCTION DRAWING: PEKERJAAN SLAB ATAP			Kecamatan : Sungai Serut, Tanjung Agung	
DIBUAT OLEH:			Kab./Kota : Kota Bengkulu	
DIPERIKSA DAN DIBETULUI OLEH:			No. Gambar : S.09.b	
MENGETAHUI:			No. Lembar :	
			Tahun 2025	No. Kontrak HK0102/Bws7.8/272/2025
			Manajer Proyek Pujiono, ST	
			Drafter Yusuf Barakka	
			Team Leader Erwin, ST	
			Supervisor Engineer Antonius Ucik, ST	
			Direksi Lapangan Franky Antonyo, ST	

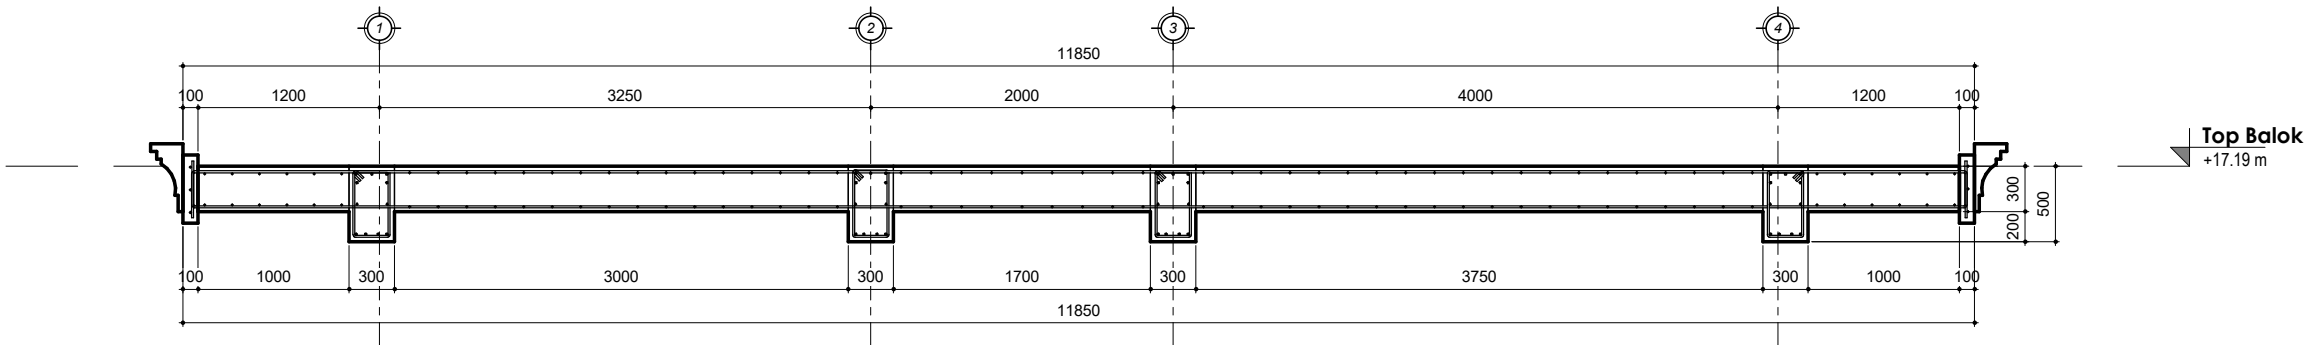

1 Detail Memanjang 1
1 : 50

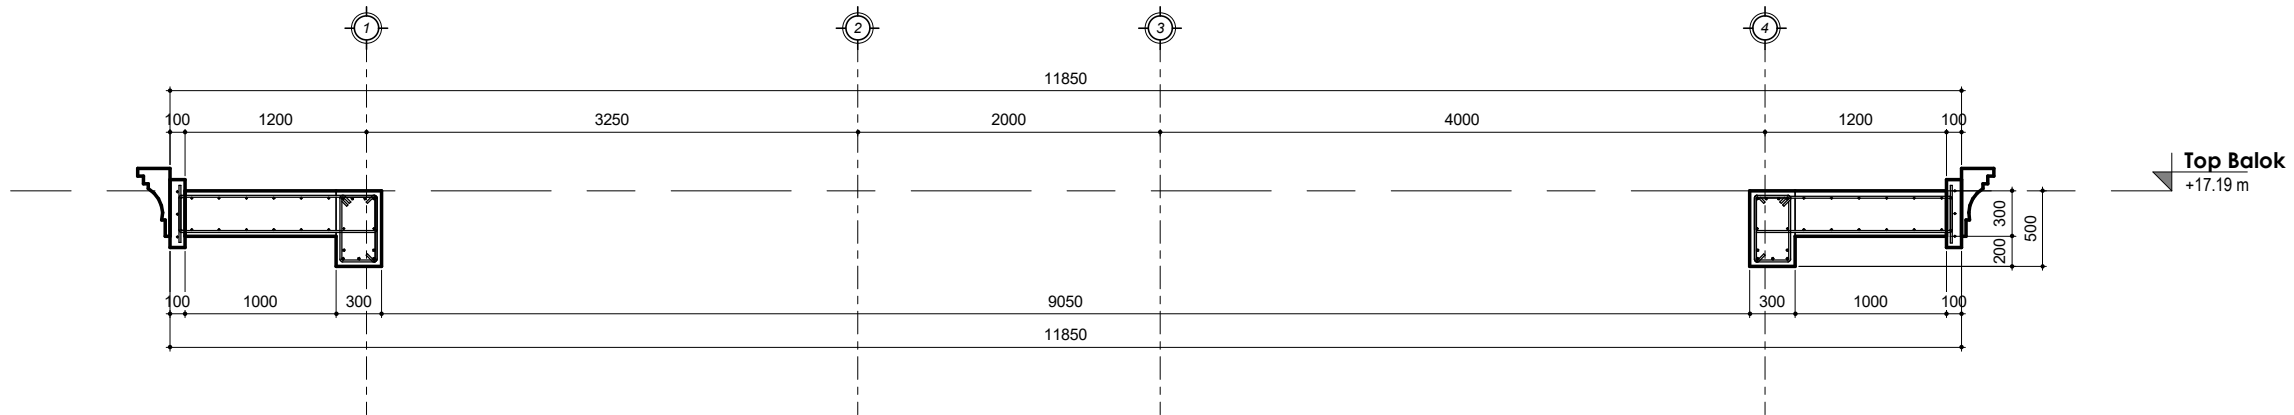


2 Detail Memanjang 2
1 : 50

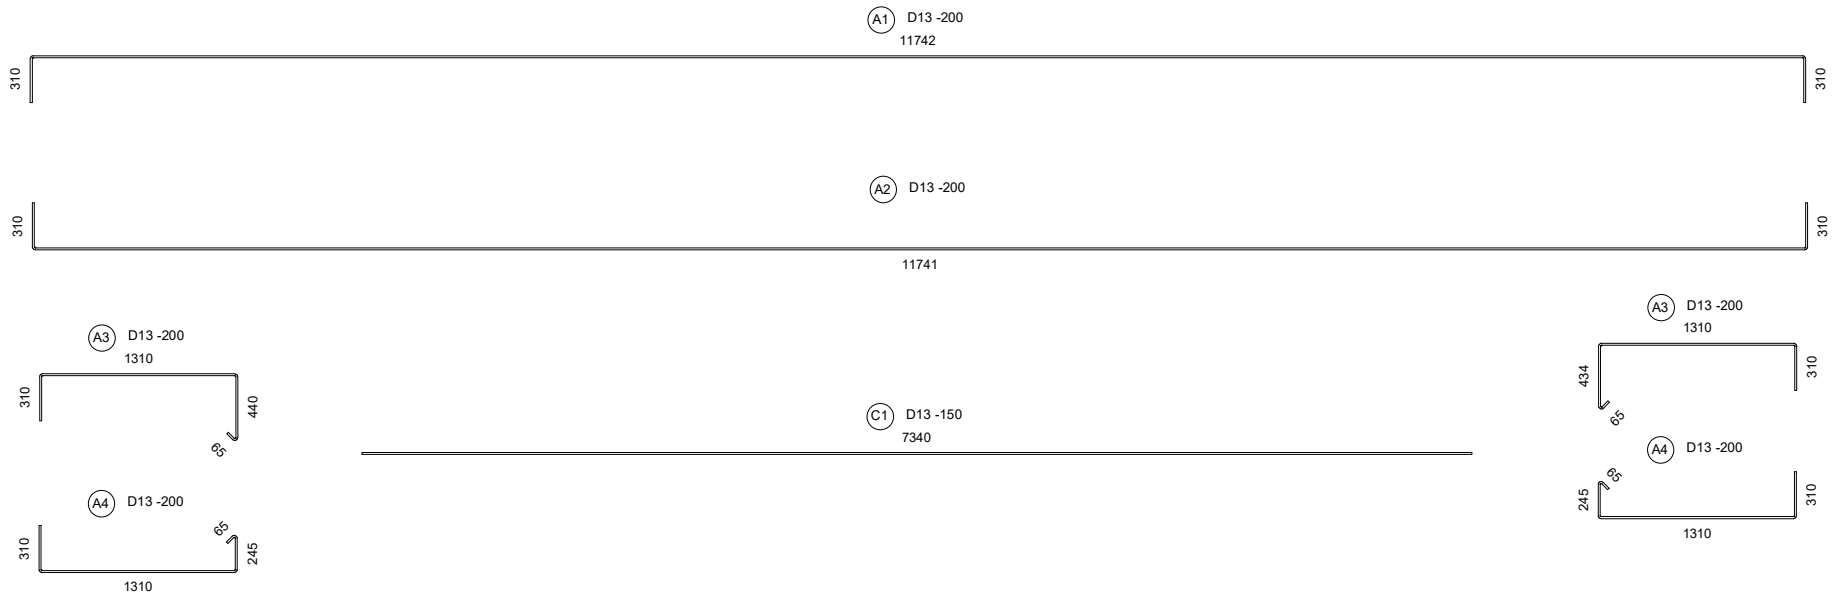


KEMENTERIAN PEKERJAAN UMUM DIREKTORAT JENDERAL SUMBER DAYA AIR BALAI WILAYAH SUNGAI SUMATERA VII BENGKULU SNVT PJSB SUMATERA VII PROVINSI BENGKULU Jl. Sungai Serut 25, Bengkulu, Telp/Fax: (0736) 541405				PROVINSI BENGKULU	
PEMBANGUNAN PENGENDALIAN BANJIR AIR BENGKULU KOTA BENGKULU				BWS SUMATERA VII BENGKULU	
CONSTRUCTION DRAWING: PEKERJAAN SLAB ATAP				Lokasi : Jl. Irian	
DIBUAT OLEH: Manajer Proyek Pujiono, ST				Kecamatan : Sungai Serut, Tanjung Agung	
DIPERIKSA DAN DIBETULUI OLEH: Drafter Yusuf Barakka				Kab./Kota : Kota Bengkulu	
Team Leader Erwin, ST				No. Gambar : S.09.c	
Supervisor Engineer Antonius Ucik, ST				No. Lembar :	
MENGETAHUI: Direksi Lapangan Franky Antonyo, ST				Tahun : 2025	
				No. Kontrak : HK0102/Bws7.8/272/2025	




SKALA				
	Yang Direvisi	Oleh	Direnc	Diset

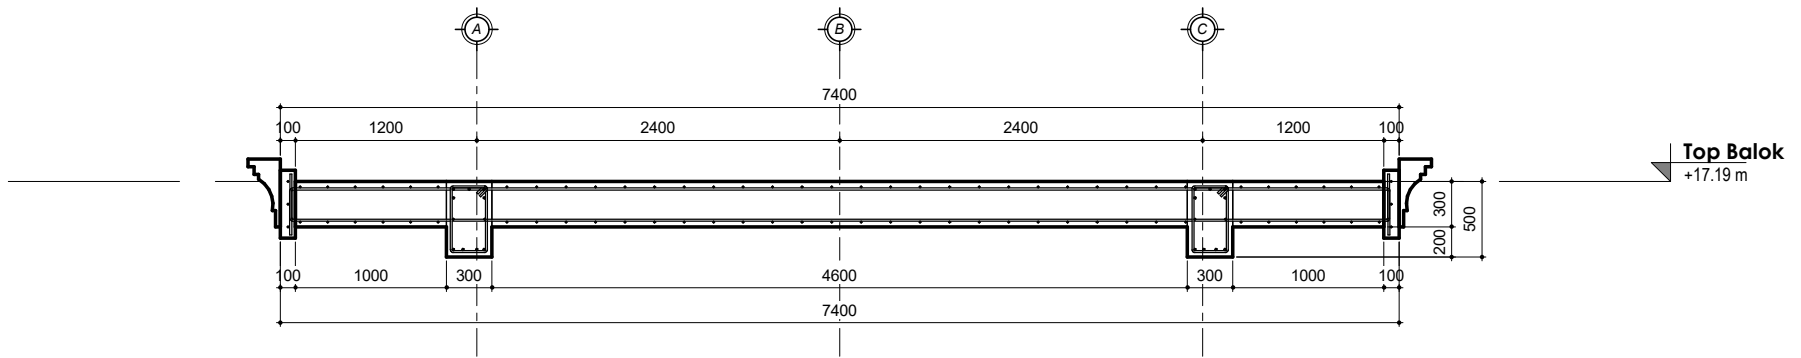

1 Detail Melintang 1
1 : 50

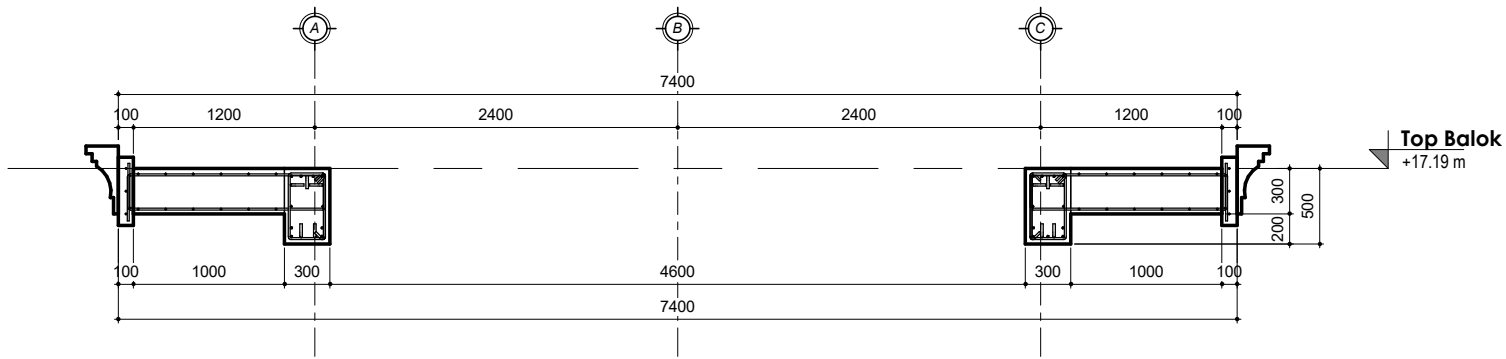

2 Detail Melintang 2
1 : 50

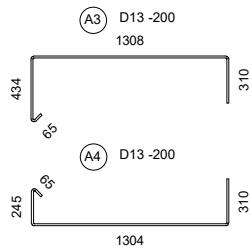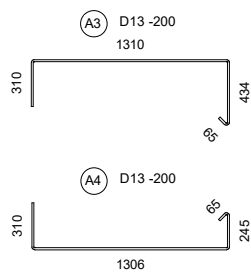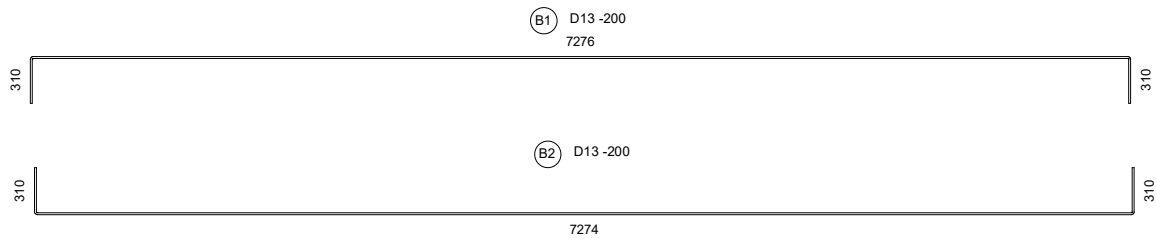

 KEMENTERIAN PEKERJAAN UMUM DIREKTORAT JENDERAL SUMBER DAYA AIR BALAI WILAYAH SUNGAI SUMATERA VII BENGKULU SNVT P.JSA, SUMATERA VII PROVINSI BENGKULU Jl. Sungai Serut, No.25, Bengkulu, 38100 Telp/Fax : (0736) 341405	PROVINSI	
	BENGKULU	
	BWS SUMATERA VII BENGKULU	
	PEMBANGUNAN PENGENDALIAN BANJIR AIR BENGKULU KOTA BENGKULU	
CONSTRUCTION DRAWING:		
PEKERJAAN SLAB ATAP		
DIBUAT OLEH:		Lokasi
DIPERIKSA DAN DIBETULKAN OLEH:		Kecamatan
MENGETAHUI:		Kab./Kota
		No. Gambar
		No. Lembar
		Tahun
		No. Kontrak
		2025
		HK0102/Bws7.8/272/2025

SKALA				
	Yang Direvisi	Oleh	Direnc	Diset

Rebar Schedule - Slab Atas					
Mark	Bar Diameter (mm)	Quantity	Bar Length (mm)	DIMENSION	Bending Detail
A1	13	6	12325	A=310 B=11742 C=0 D=0 E=0 F=0	
A1	13	6	12325	A=310 B=11742 C=0 D=0 E=0 F=0	
A2	13	6	12323	A=310 B=11741 C=0 D=0 E=0 F=0	
A2	13	6	12323	A=310 B=11741 C=0 D=0 E=0 F=0	
A3	13	24	2088	A=310 B=1310 C=440 D=65 E=0 F=0	
A3	13	24	2082	A=310 B=1310 C=434 D=65 E=0 F=0	
A3	13	16	2079	A=310 B=1308 C=434 D=65 E=0 F=0	
A3	13	9	2079	A=310 B=1308 C=434 D=65 E=0 F=0	
A3	13	20	2079	A=310 B=1308 C=434 D=65 E=0 F=0	
A3	13	16	2081	A=310 B=1310 C=434 D=65 E=0 F=0	
A3	13	9	2081	A=310 B=1310 C=434 D=65 E=0 F=0	
A3	13	20	2081	A=310 B=1310 C=434 D=65 E=0 F=0	
A4	13	24	1893	A=310 B=1310 C=245 D=65 E=0 F=0	
A4	13	24	1893	A=310 B=1310 C=245 D=65 E=0 F=0	
A4	13	16	1887	A=310 B=1304 C=245 D=65 E=0 F=0	

Rebar Schedule - Slab Atas					
Mark	Bar Diameter (mm)	Quantity	Bar Length (mm)	DIMENSION	Bending Detail
A4	13	9	1887	A=310 B=1304 C=245 D=65 E=0 F=0	
A4	13	20	1887	A=310 B=1304 C=245 D=65 E=0 F=0	
A4	13	16	1889	A=310 B=1306 C=245 D=65 E=0 F=0	
A4	13	9	1889	A=310 B=1306 C=245 D=65 E=0 F=0	
A4	13	20	1889	A=310 B=1306 C=245 D=65 E=0 F=0	
B1	13	6	7859	A=310 B=7276 C=0 D=0 E=0 F=0	
B1	13	6	7859	A=310 B=7276 C=0 D=0 E=0 F=0	
B2	13	6	7857	A=310 B=7274 C=0 D=0 E=0 F=0	
B2	13	6	7857	A=310 B=7274 C=0 D=0 E=0 F=0	
C1	13	3	7340	A=0 B=7340 C=0 D=0 E=0 F=0	
C1	13	3	7340	A=0 B=7340 C=0 D=0 E=0 F=0	
C2	13	3	11790	A=0 B=11790 C=0 D=0 E=0 F=0	
C2	13	3	11790	A=0 B=11790 C=0 D=0 E=0 F=0	
Grand total: 28		336	150756		

SKALA				
	Yang Direvisi	Oleh	Direnc	Diset

 KEMENTERIAN PEKERJAAN UMUM DIREKTORAT JENDERAL SUMBER DAYA AIR BALAI WILAYAH SUNGAI SUMATERA VII BENGKULU SNVT PJSB SUMATERA VII PROVINSI BENGKULU Jl. Sungai Serut, Bengkulu 36100, Indonesia				PROVINSI BENGKULU	
				BWS SUMATERA VII BENGKULU	
PEMBANGUNAN PENGENDALIAN BANJIR AIR BENGKULU KOTA BENGKULU				Lokasi : Jl. Irian	
CONSTRUCTION DRAWING: PEKERJAAN SLAB ATAP				Kecamatan : Sungai Serut, Tanjung Agung	
DIBUAT OLEH:		Manajer Proyek	Pujiono, ST	Kab./Kota : Kota Bengkulu	
DIPERIKSA DAN DIBETULI OLEH:		Drafter	Yusuf Barakka	No. Gambar : S.09.e	
		Team Leader	Erwin, ST	No. Lembar :	
MENGETAHUI:		Supervisor Engineer	Antonius Ucik, ST	Tahun 2025	
		Direksi Lapangan	Franky Antonyo, ST	No. Kontrak HK0102/Bws7.8/272/2025	